



Irigare prin picurare — ansamblu, scara 1:350

Cele 8 zone (vane), conducta principală (linie neagră întreruptă, traseu orientativ de la sursă la fiecare vană) și liniile de picurare (culoarea zonei, lungime estimată ca arbore de acoperire minim între plante). Cifra din fiecare cerc = numărul de picurătoare de 4 l/h la planta aceea. Sursa: colțul de sud-est al casei, între casă și magazin.

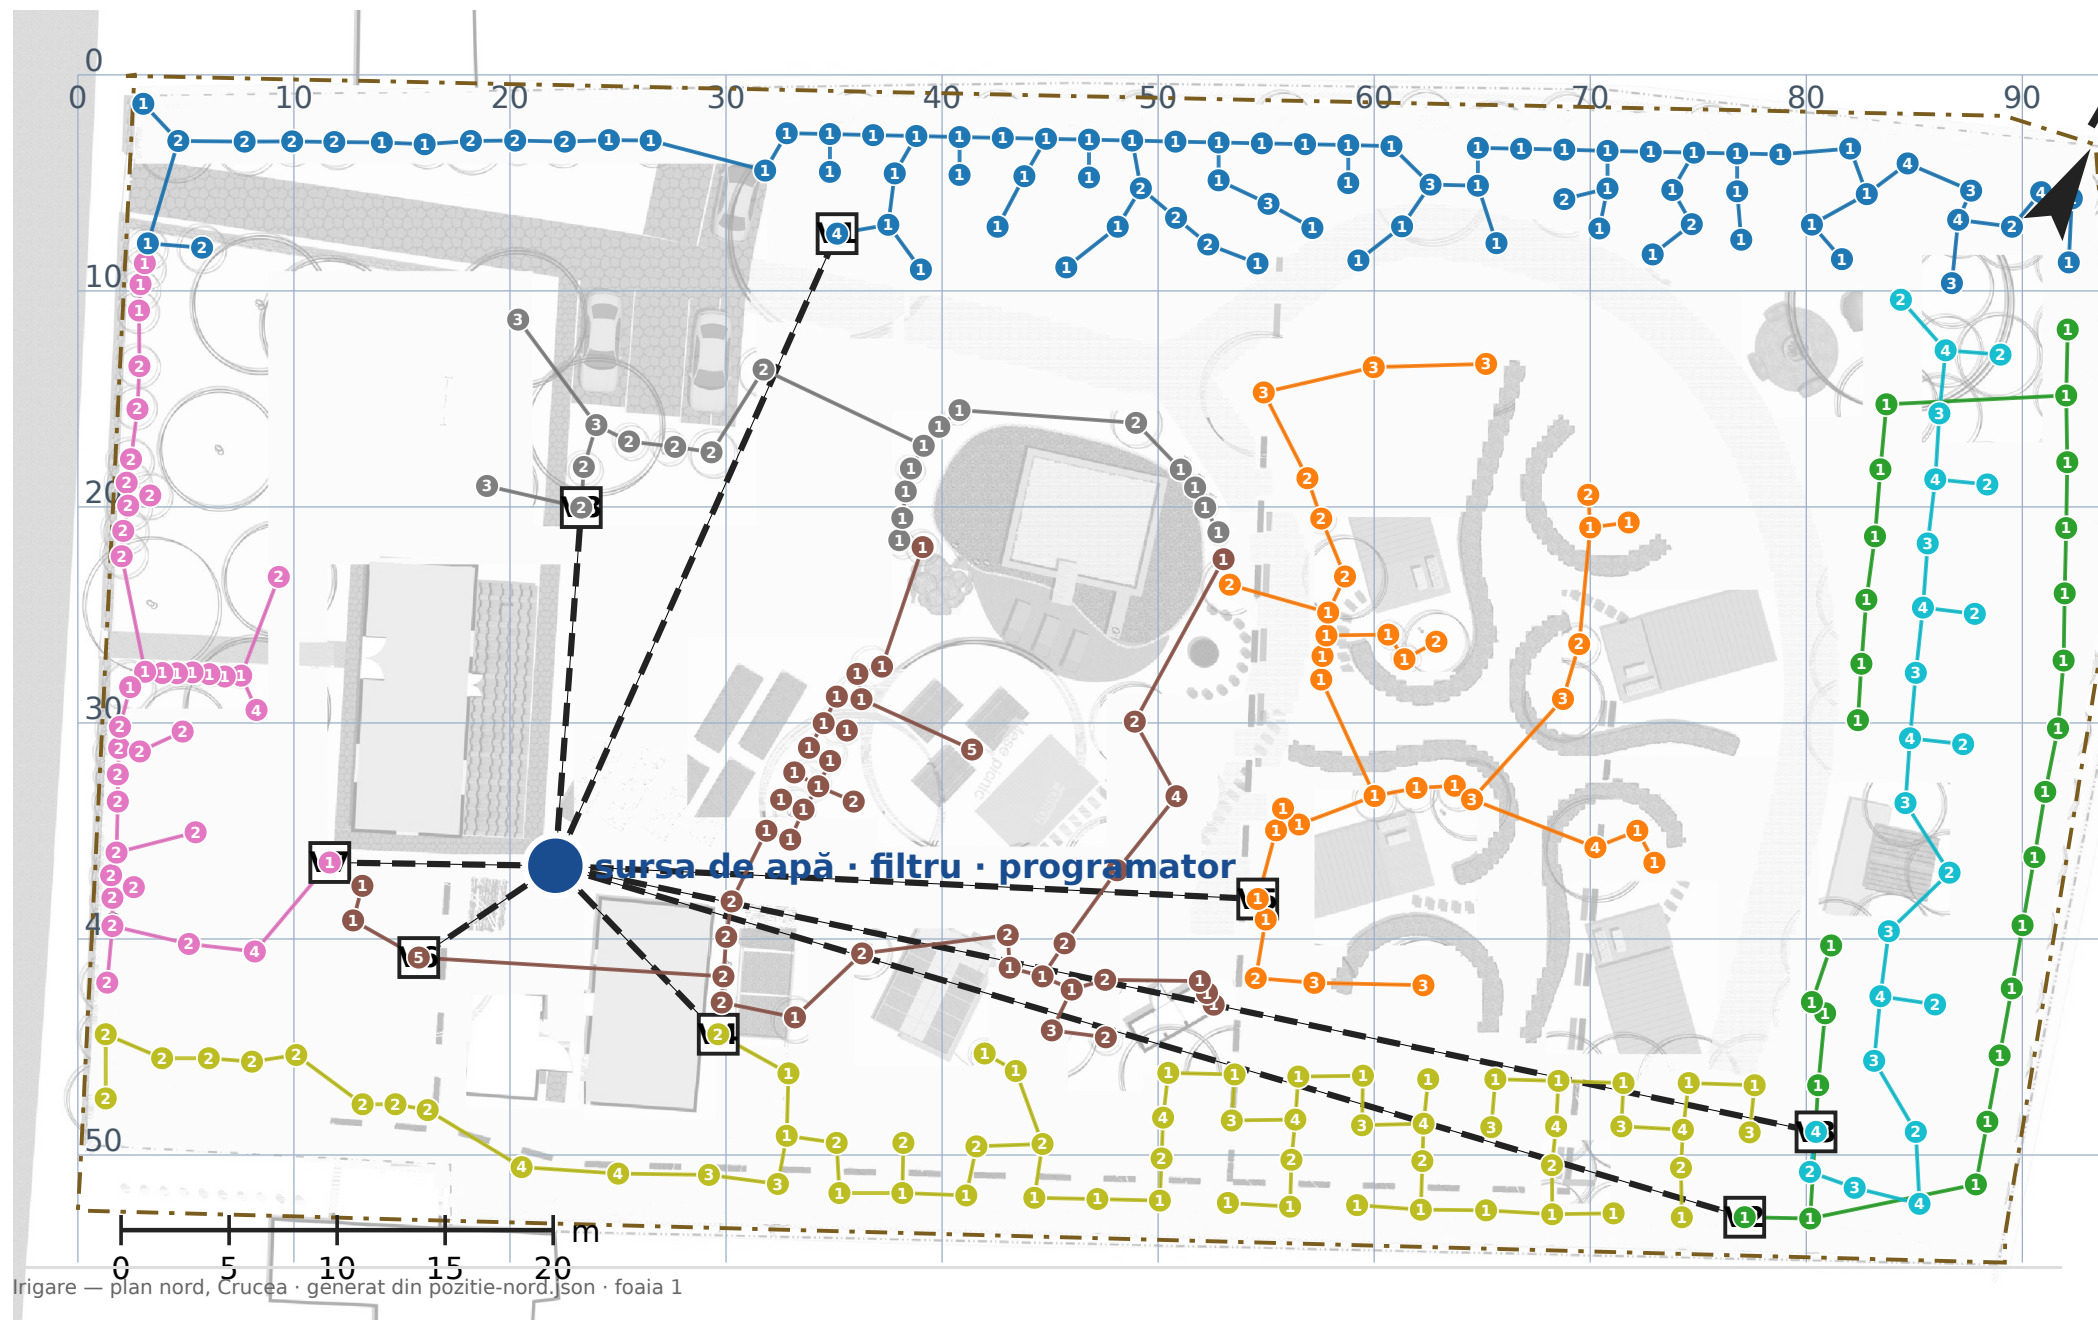


Irigare — cadran 1, scara 1:200

Aceleași cadrane ca în fișele de plantare. Cerc colorat = zona (vana) plantei, cifra = picurătoare de 4 l/h, eticheta = planta. Liniile colorate = tub de 16 mm pe zonă; linia neagră întreruptă = conducta principală de 32 mm.

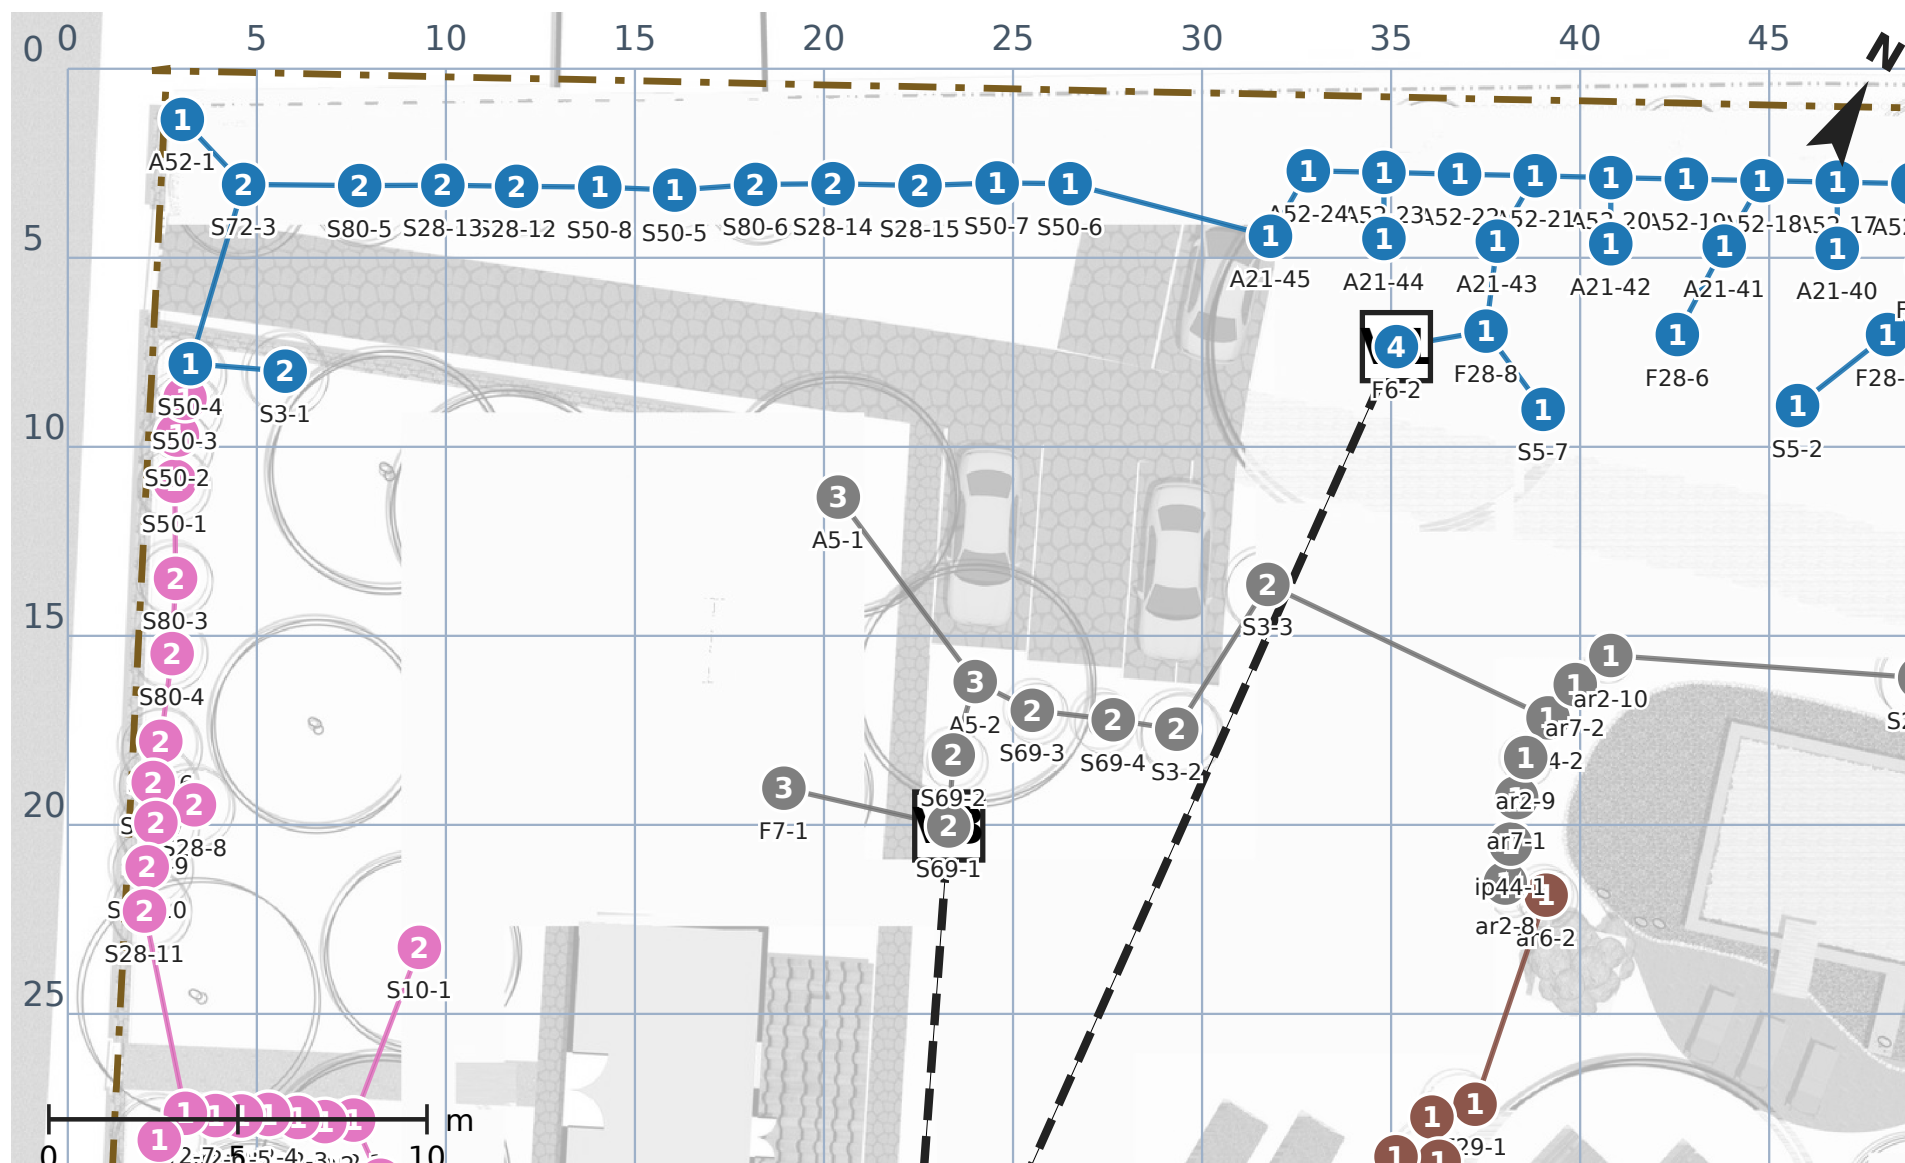


Irigare – cadran 2, scara 1:200

Aceleași cadrane ca în fișele de plantare. Cerc colorat = zona (vana) plantei, cifra = picurătoare de 4 l/h, eticheta = planta. Liniile colorate = tub de 16 mm pe zonă; linia neagră întreruptă = conducta principală de 32 mm.

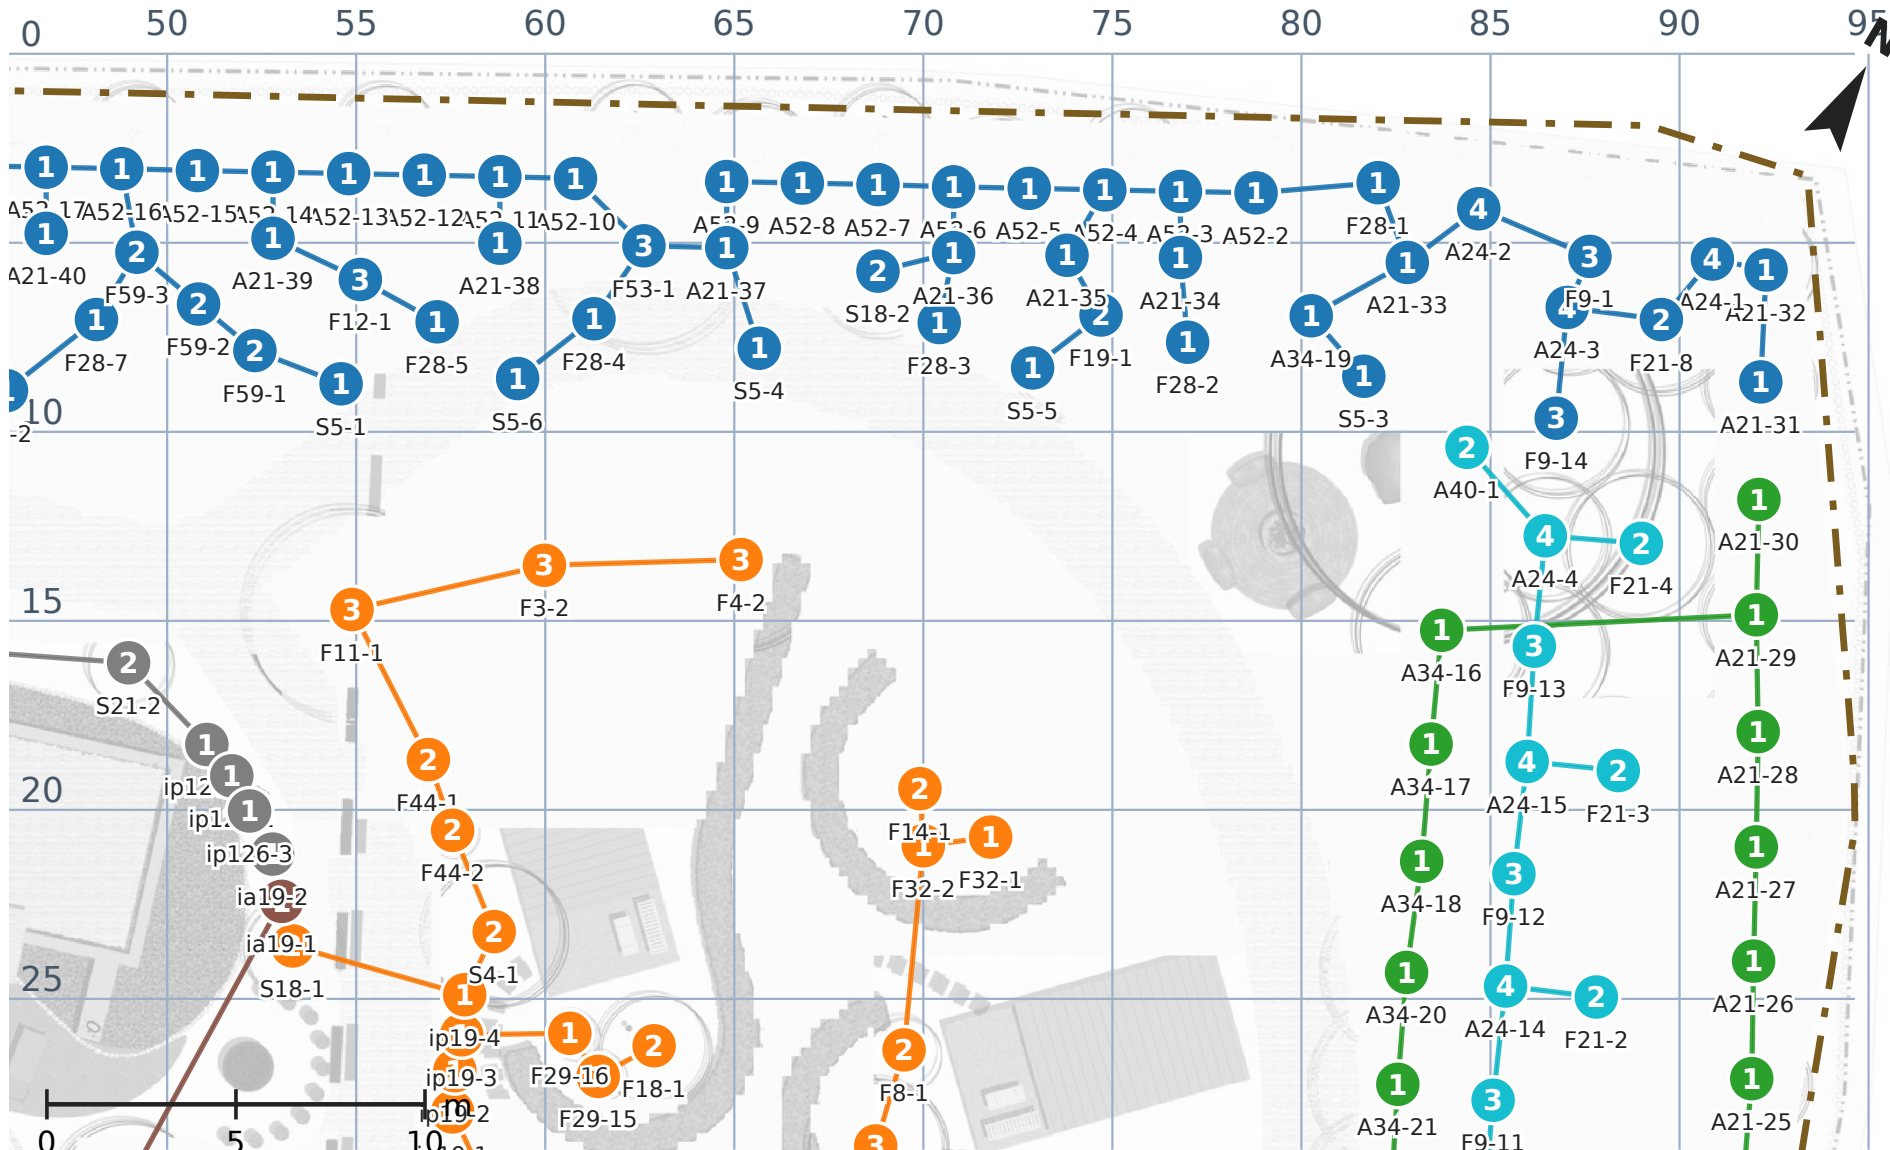


Irigare – cadran 3, scara 1:200

Aceleași cadrane ca în fișele de plantare. Cerc colorat = zona (vana) plantei, cifra = picurătoare de 4 l/h, eticheta = planta. Liniile colorate = tub de 16 mm pe zonă; linia neagră întreruptă = conducta principală de 32 mm.

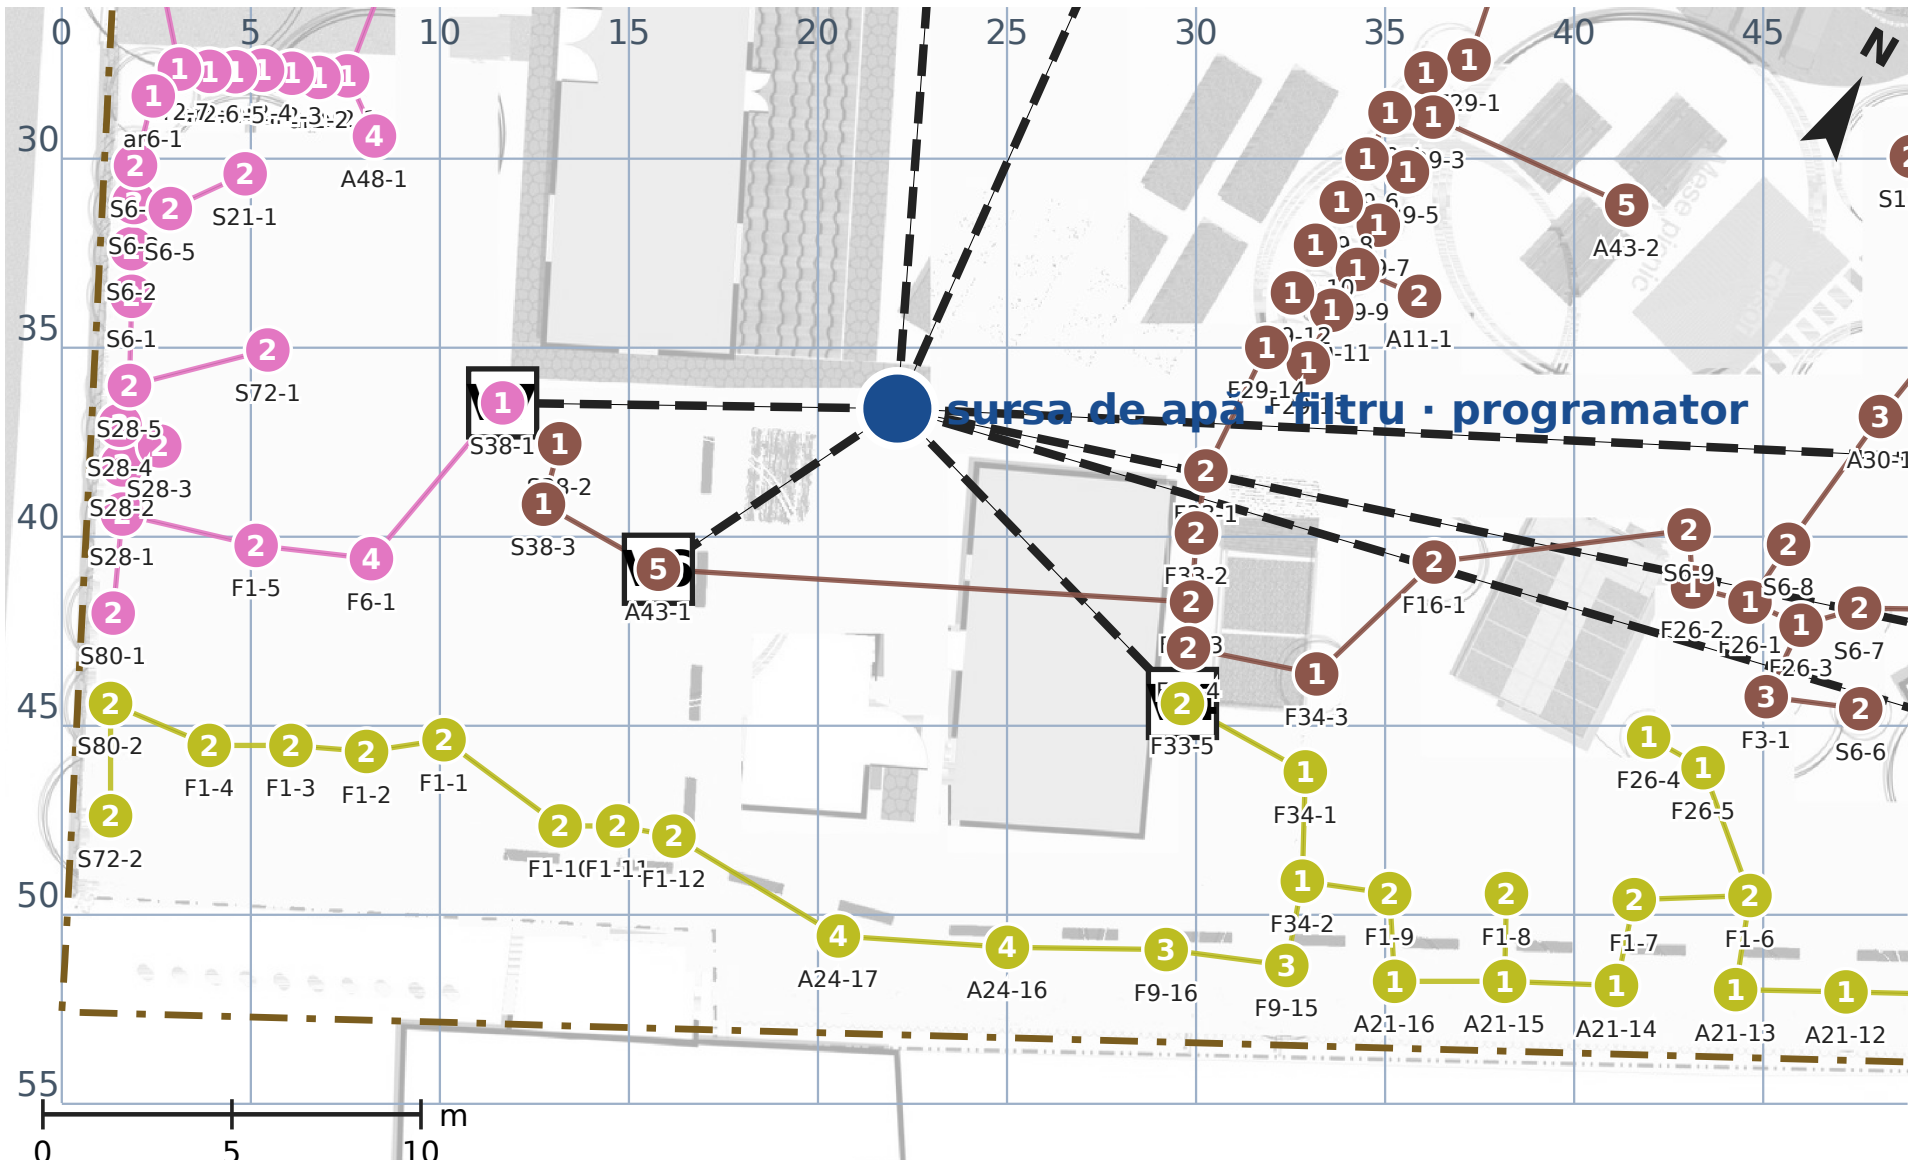

Irigare — cadran 4, scara 1:200

Aceleași cadrane ca în fișele de plantare. Cerc colorat = zona (vana) plantei, cifra = picurătoare de 4 l/h, eticheta = planta. Liniile colorate = tub de 16 mm pe zonă; linia neagră întreruptă = conducta principală de 32 mm.

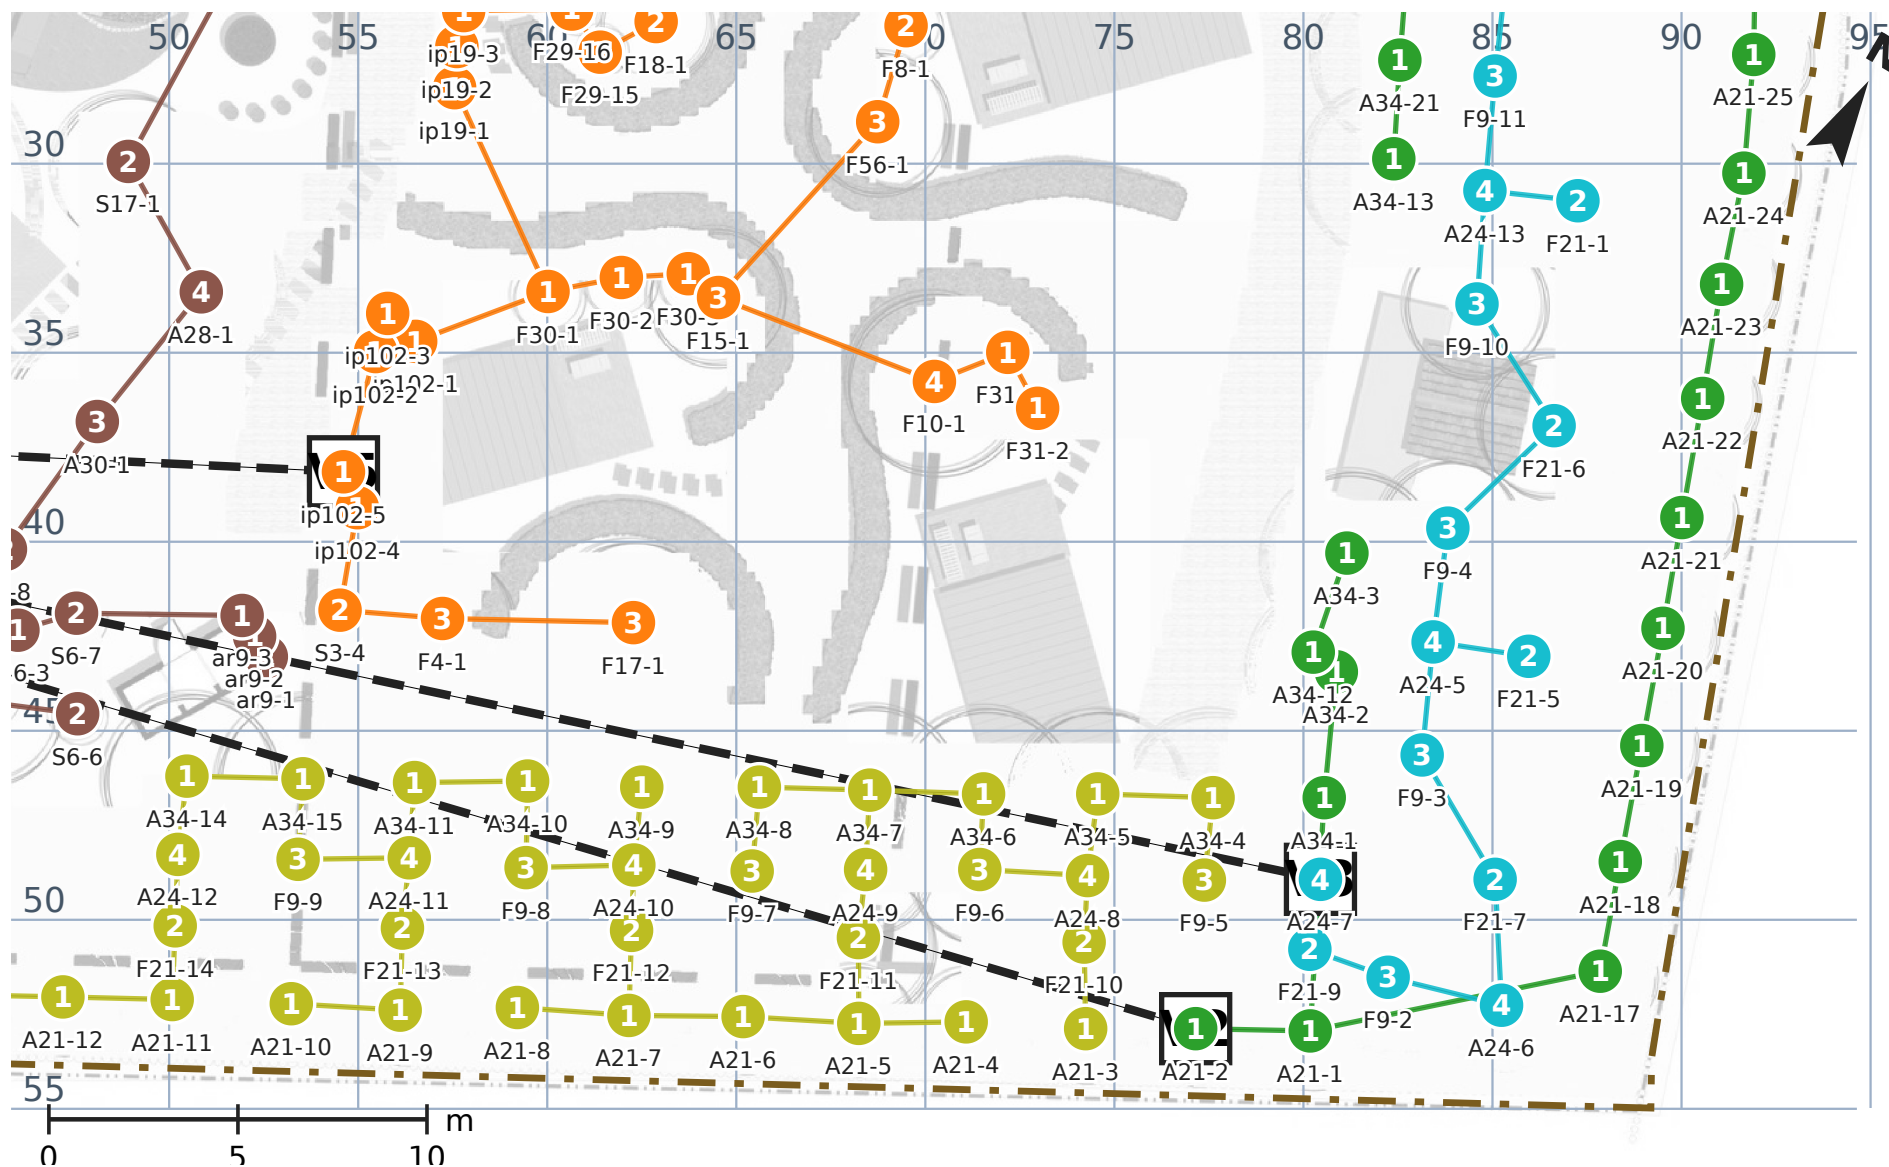

Irigare — tabelul pe vane, programe, materiale

Lungimile sunt estimate din pozițiile plantelor (tub de 16 mm = arbore de acoperire minim + 15 %; principala = distanța dreaptă de la sursă + 25 %). Picurătoare: 1 pentru doze de 2-5 l, 2 pentru 8-15 l, 3 pentru 20-25 l, 4 pentru 30 l, 5 pentru 40 l.

Vană	Zonă	Prog.	Plante	Picurătoare	Debit l/h	Udare	l/săpt. (an 3+)	Tub 16 mm (m)	Principală (m)	Plante din zonă
V1	Perdeaua de nord	A	82	116	464	75 min × 1/săpt	580	209	40	Ulm de Turkestan 24 Sălcioară 15 Măceș 8 Păducel 7 Kerria 5 Ploaie de aur 4 Frasin 3 Aronia 3 Dud alb 2 Liliac de vară 2 Corn 1 Iasomie falsă 1 Pin negru 1 Pom de stafide 1 Prun 1 Soc 1 Vișin 1 Nuc 1 Călin 1
V2	Est — linia uscată	A	26	26	104	75 min × 1/săpt	130	100	72	Sălcioară 16 Pin negru 10
V3	Est — linia udă (frasini)	C	23	67	268	120 min × 2/săpt	1 072	74	75	Corn 8 Frasin 7 Dud alb 7 Stejar pufos 1
V4	Latura de sud	A	61	115	460	75 min × 1/săpt	575	180	14	Sălcioară 14 Alun 11 Pin negru 10 Frasin 7 Dud alb 7 Corn 5 Arbore de mazăre 2 Cătină 2 Liliac de vară 1 Călin 1 Viță de vie 1
V7	Stradă și terasă	B	37	66	264	75 min × 2/săpt	660	76	13	Ploaie de aur 11 Lavandă 7 Hibiscus 5 Liliac de vară 3 Kerria 3 Alun 1 Cununiță 1 Călin 1 Rozmarin 1 Tei argintiu 1 Liliac 1 Nuc 1 Salcâm galben 1
V5	Labirint și căsuțe	B	34	59	236	75 min × 2/săpt	590	108	41	Lofantus 5 Tătăneasă 4 Coacăz negru 3 Smochin 2 Sânger 2 Agriș 2 Coacăz roșu 2 Coacăz alb 2 Păr 1 Piersic 1 Soc 1 Kaki 1 Migdal 1 Nectarin 1 Moșmon 1 Jujuba 1 Corcoduș 1 Scumpie 1 Cireș 1 Iasomie falsă 1
V6	Grădina de bucătărie casă	B	41	67	268	75 min × 2/săpt	670	128	10	Coacăz roșu 14 Viță de vie 4 Hibiscus 4 Cătină 3 Roiniță 3 Cununiță 2 Salcie plângătoare 2 Arbore de mazăre 1 Kaki 1 Arborele de lalea 1 Magnolie 1 Oțetar 1 Rozmarin 1 Fenicul 1 Arborele de mătase 1 Rodiu 1
V8	Pajiștea — pomi răzleți	C	21	34	136	120 min × 2/săpt	544	62	21	Trandafir de Rescht 4 Lavandă 3 Potentilla 3 Paltin de câmp 2 Iasomie falsă 2 Isop 2 Salvie 2 Măr 1 Fenicul 1 Liliac 1
Total			325	550			4 821	938	284	

Programe la programator

Program	Vane	Anul 1 (plantare)	Anul 2	Din anul 3
A secetă	V1, V2, V4	2 × / săpt, 110 min	1 × / săpt, 95 min	1 × / săpt, 75 min (5 l la o picurătoare)
B arbuști	V5, V6, V7	3 × / săpt, 110 min	2 × / săpt, 95 min	2 × / săpt, 75 min
C pomi și arbori	V3, V8	3 × / săpt, 180 min	2 × / săpt, 150 min	2 × / săpt, 120 min

Udarea se face noaptea sau dimineata devreme, o singură vană odată (programatorul le pornește pe rând). Din mai până în septembrie; se sare peste săptămânile cu peste 15 mm de ploaie. Plantele „setoase” aflate în zonele A (corn, alun, soc, duzi de pe nord) au 2-3 picurătoare și primesc doza dublă o dată pe săptămână — compromis acceptabil pentru arbuști și arbori tineri.

Materiale (orientativ)

Material	Cantitate	Observații
Conductă principală PE 32 mm PN6	350 m	îngropată 30-40 cm cu rezervă de 10 %; traseul real urmează aleile nu linia dreaptă din schemă
Tub orb PE 16 mm	1100 m	la suprafață sub mulci; se fixează cu agrafe la 2 m
Picurătoare autocompensante 4 l/h cu cui	650 buc	autocompensante obligatoriu — liniile au peste 50 m și teren cu pantă mică
Electrovane 1" 24 V AC	8	în 2-3 cămine de vane la capătul fiecărei zone
Programator 8 zone 24 V	1	la sursă în magazie; senzor de ploaie recomandat
Filtru cu discuri 1" 120 mesh + reductor de presiune 1 5-2 bar	1 + 1	la sursă înaintea programatorului
Cablu 24 V multifilar (9 fire)	350 m	în același șanț cu principala
Fitinguri 32 mm (teuri coturi mufe robineti de golire) fittinguri 16 mm dopuri de capăt agrafe	set	robinet de golire la punctul cel mai jos al fiecărei zone pentru iarnă

Debitul maxim pe o vană: 464 l/h — sub debitul unui robinet obișnuit de 3/4" (1 500-2 000 l/h) deci fără pompă dacă presiunea la sursă e peste 2 bar. Consumul total din anul 3: ≈ 4 821 l pe săptămână 106 mc pe sezon ≈ 1 055 lei la tariful RAJA.