


Plan nord — foaia de ansamblu, scara 1:500


Toată parcela (91,5 × 51,6 m) așezată cu latura lungă orizontal; nordul e la 30° spre dreapta față de sus (vezi săgeata), strada e pe latura din stânga (vest), gardul de nord e latura de sus. Cele 4 cadrane sunt foile 2-5 la scara 1:200. Rețeaua are 10 m; originea (0,0) e colțul din stânga-sus al dreptunghiului care încadrează parcela, x crește spre est, y spre sud. Linia punctată maro e hotarul.

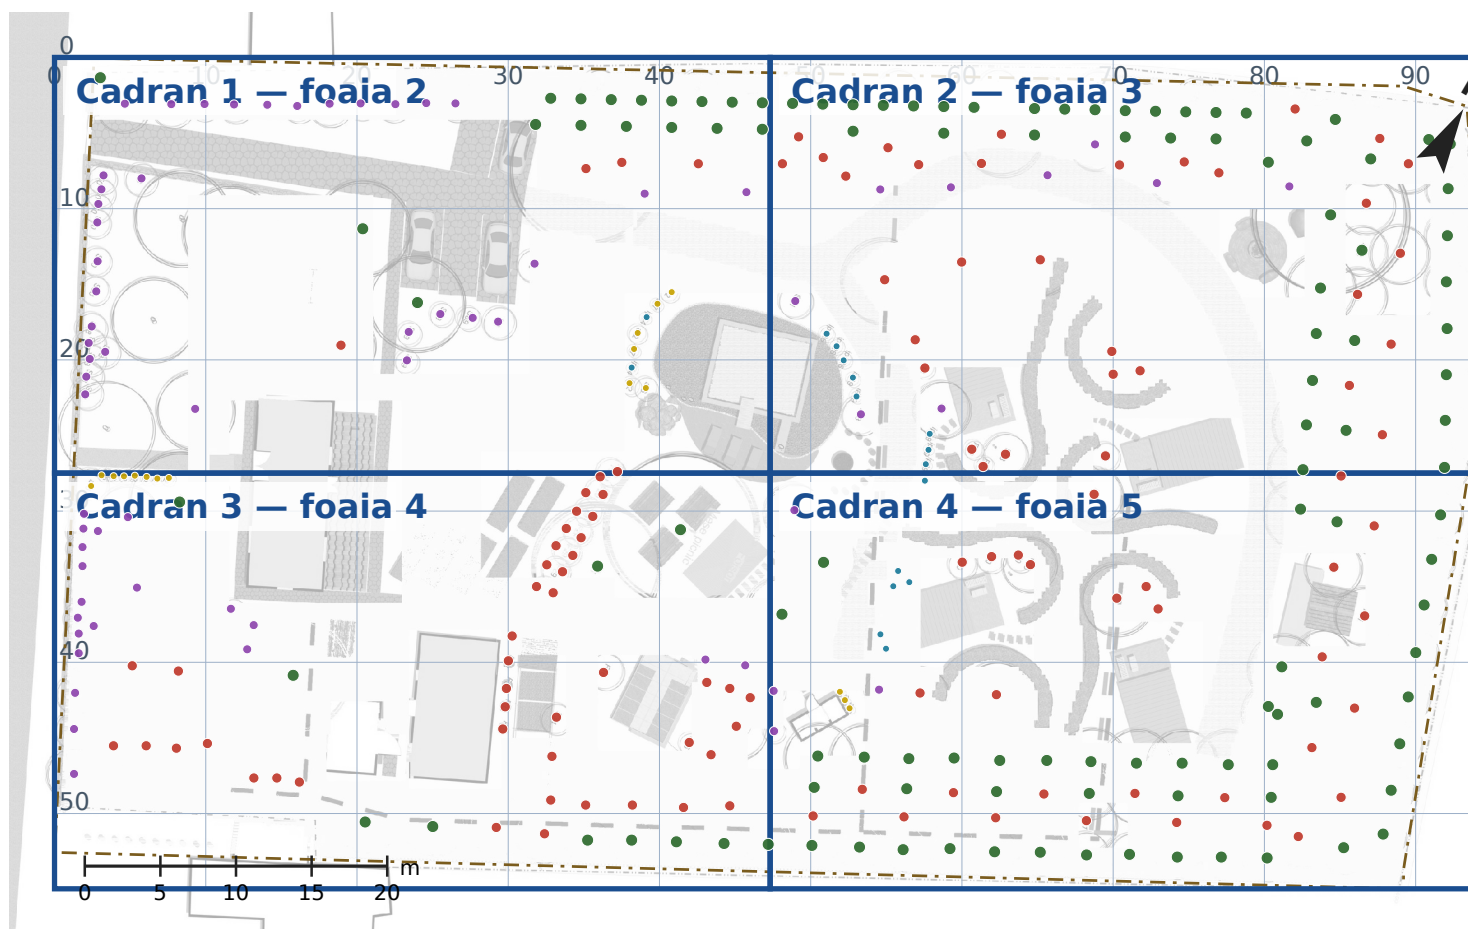

● Arbore 116 ● Fructifer 110 ● Arbust 66 ● Aromatică 17 ● Ierbacee 16 · 325 plante


Cadran 1 — scara 1:200 (1 cm = 2 m)

63 plante în cadran. Eticheta = cod specie și număr (ex. A21-14). Linia punctată neagră cu cifră = distanța în metri până la cel mai apropiat exemplar din aceeași specie. Linia portocalie = distanța până la gard. Rețea de 5 m, coordonatele în metri ca pe foaia 1. Marginea suprapune 1,5 m peste cadranul vecin.

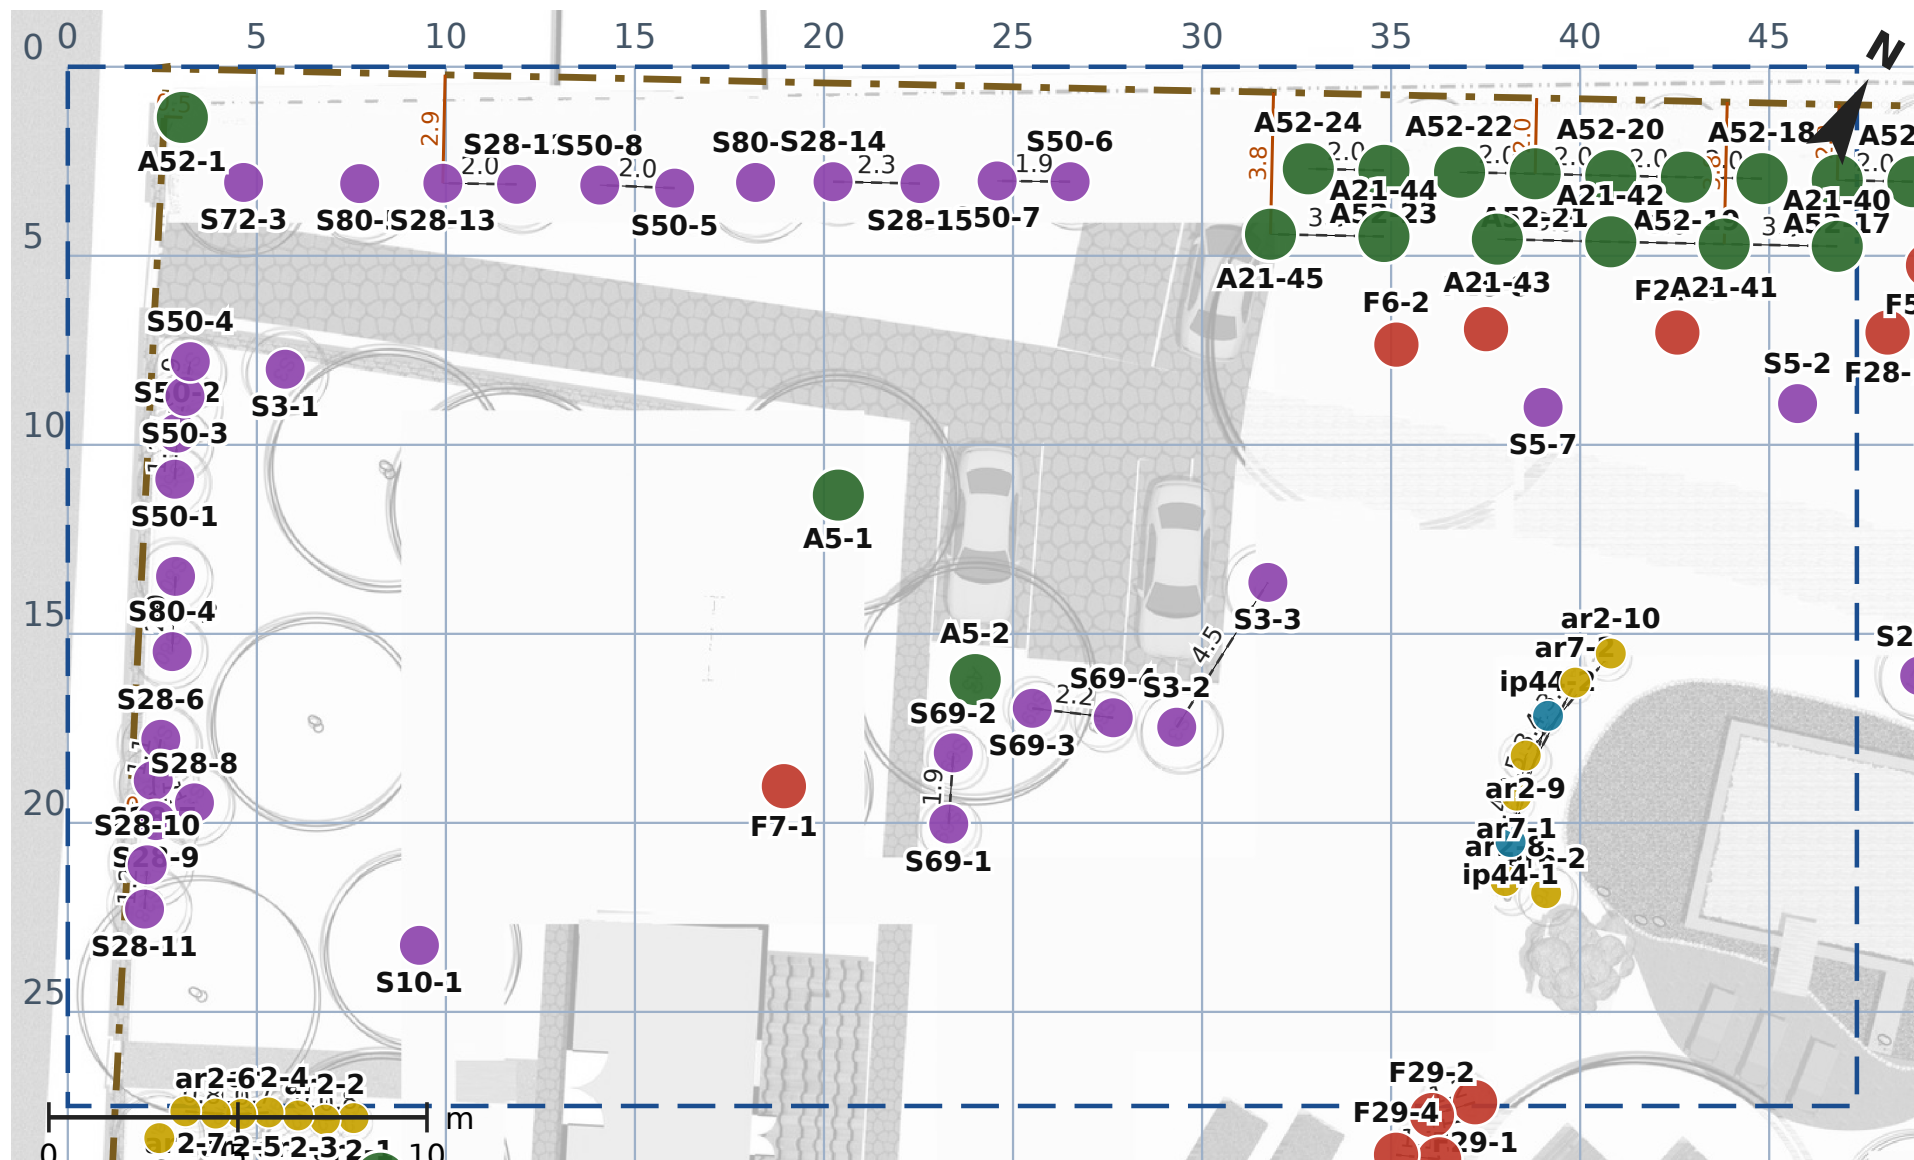


Cadran 2 – scara 1:200 (1 cm = 2 m)

92 plante în cadran. Eticheta = cod specie și număr (ex. A21-14). Linia punctată neagră cu cifră = distanța în metri până la cel mai apropiat exemplar din aceeași specie. Linia portocalie = distanța până la gard. Rețea de 5 m, coordonatele în metri ca pe foaia 1. Marginea suprapune 1,5 m peste cadranul vecin.

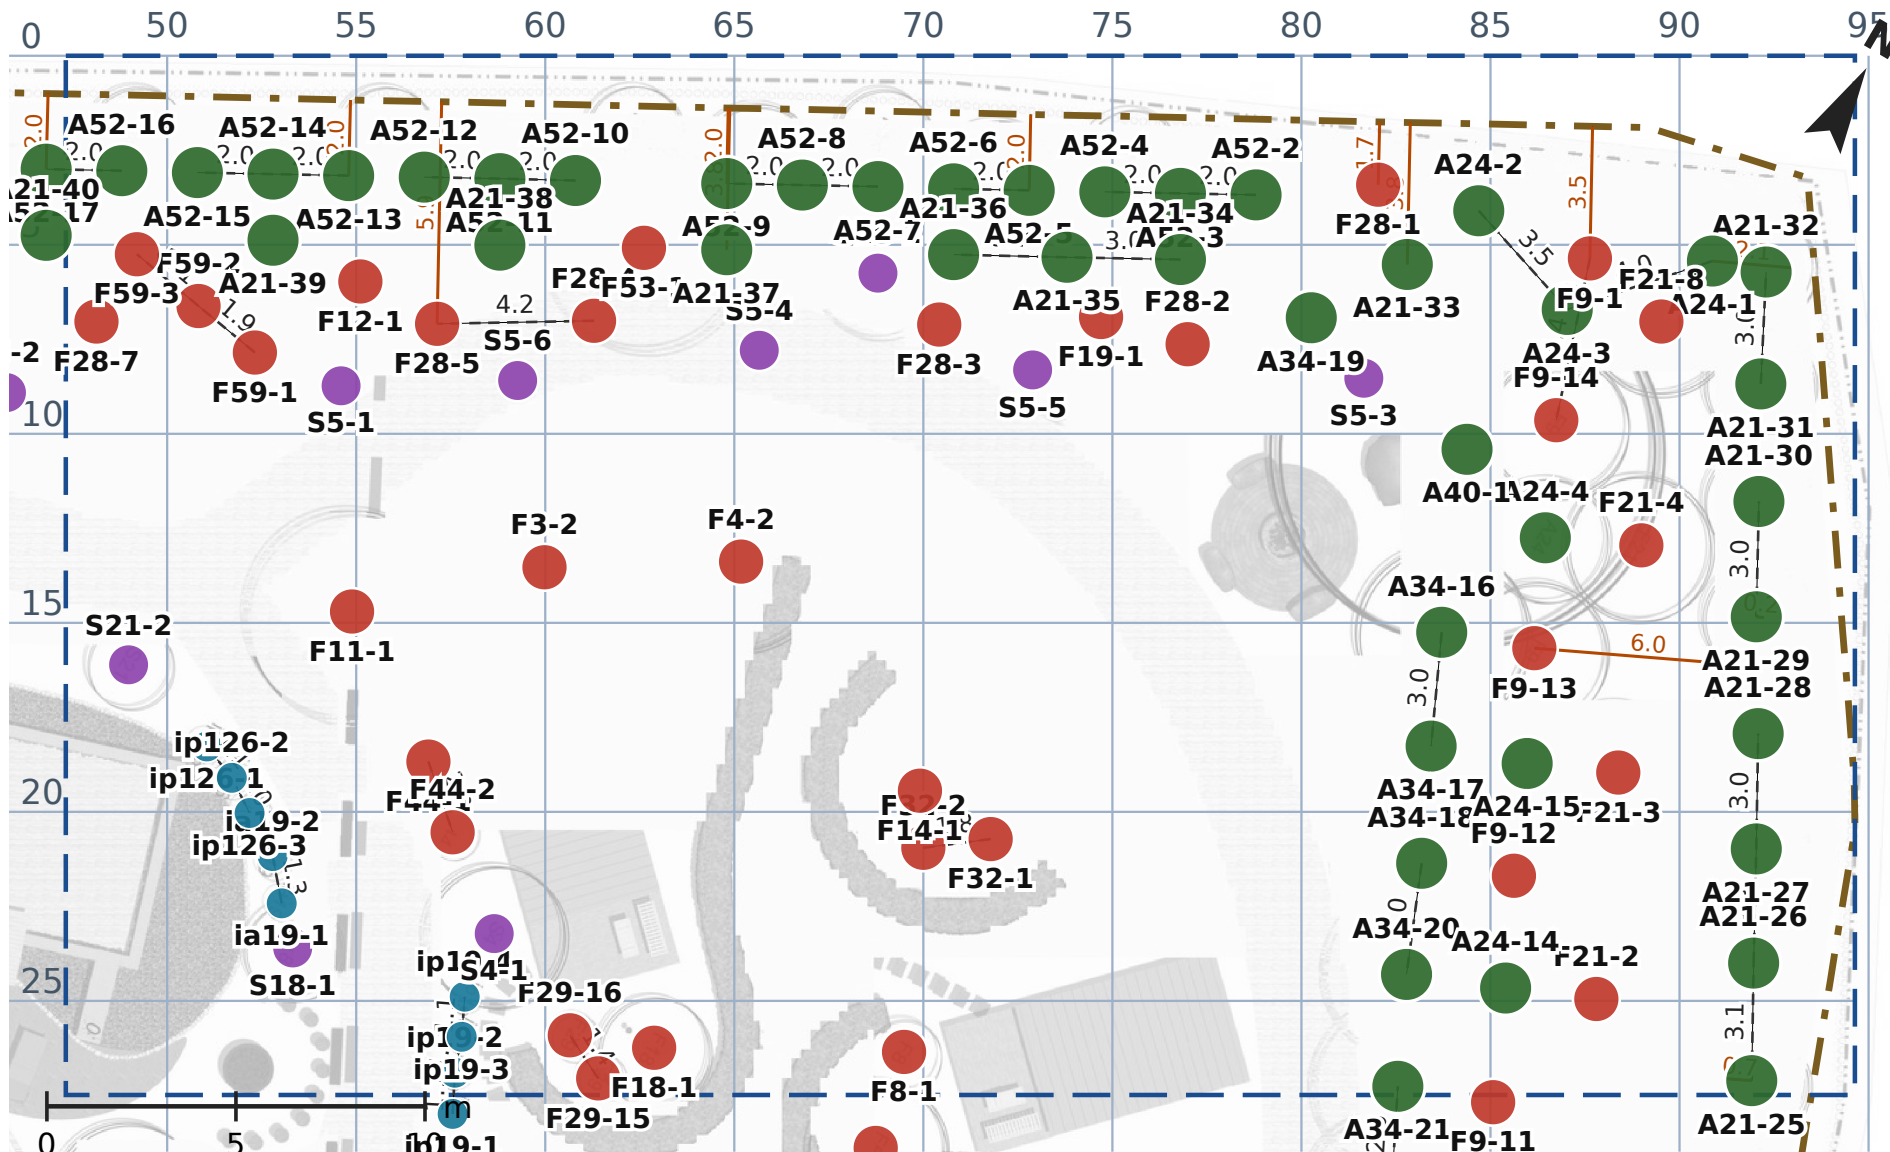


Cadran 3 — scara 1:200 (1 cm = 2 m)

82 plante în cadran. Eticheta = cod specie și număr (ex. A21-14). Linia punctată neagră cu cifră = distanța în metri până la cel mai apropiat exemplar din aceeași specie. Linia portocalie = distanța până la gard. Rețea de 5 m, coordonatele în metri ca pe foaia 1. Marginea suprapune 1,5 m peste cadranul vecin.

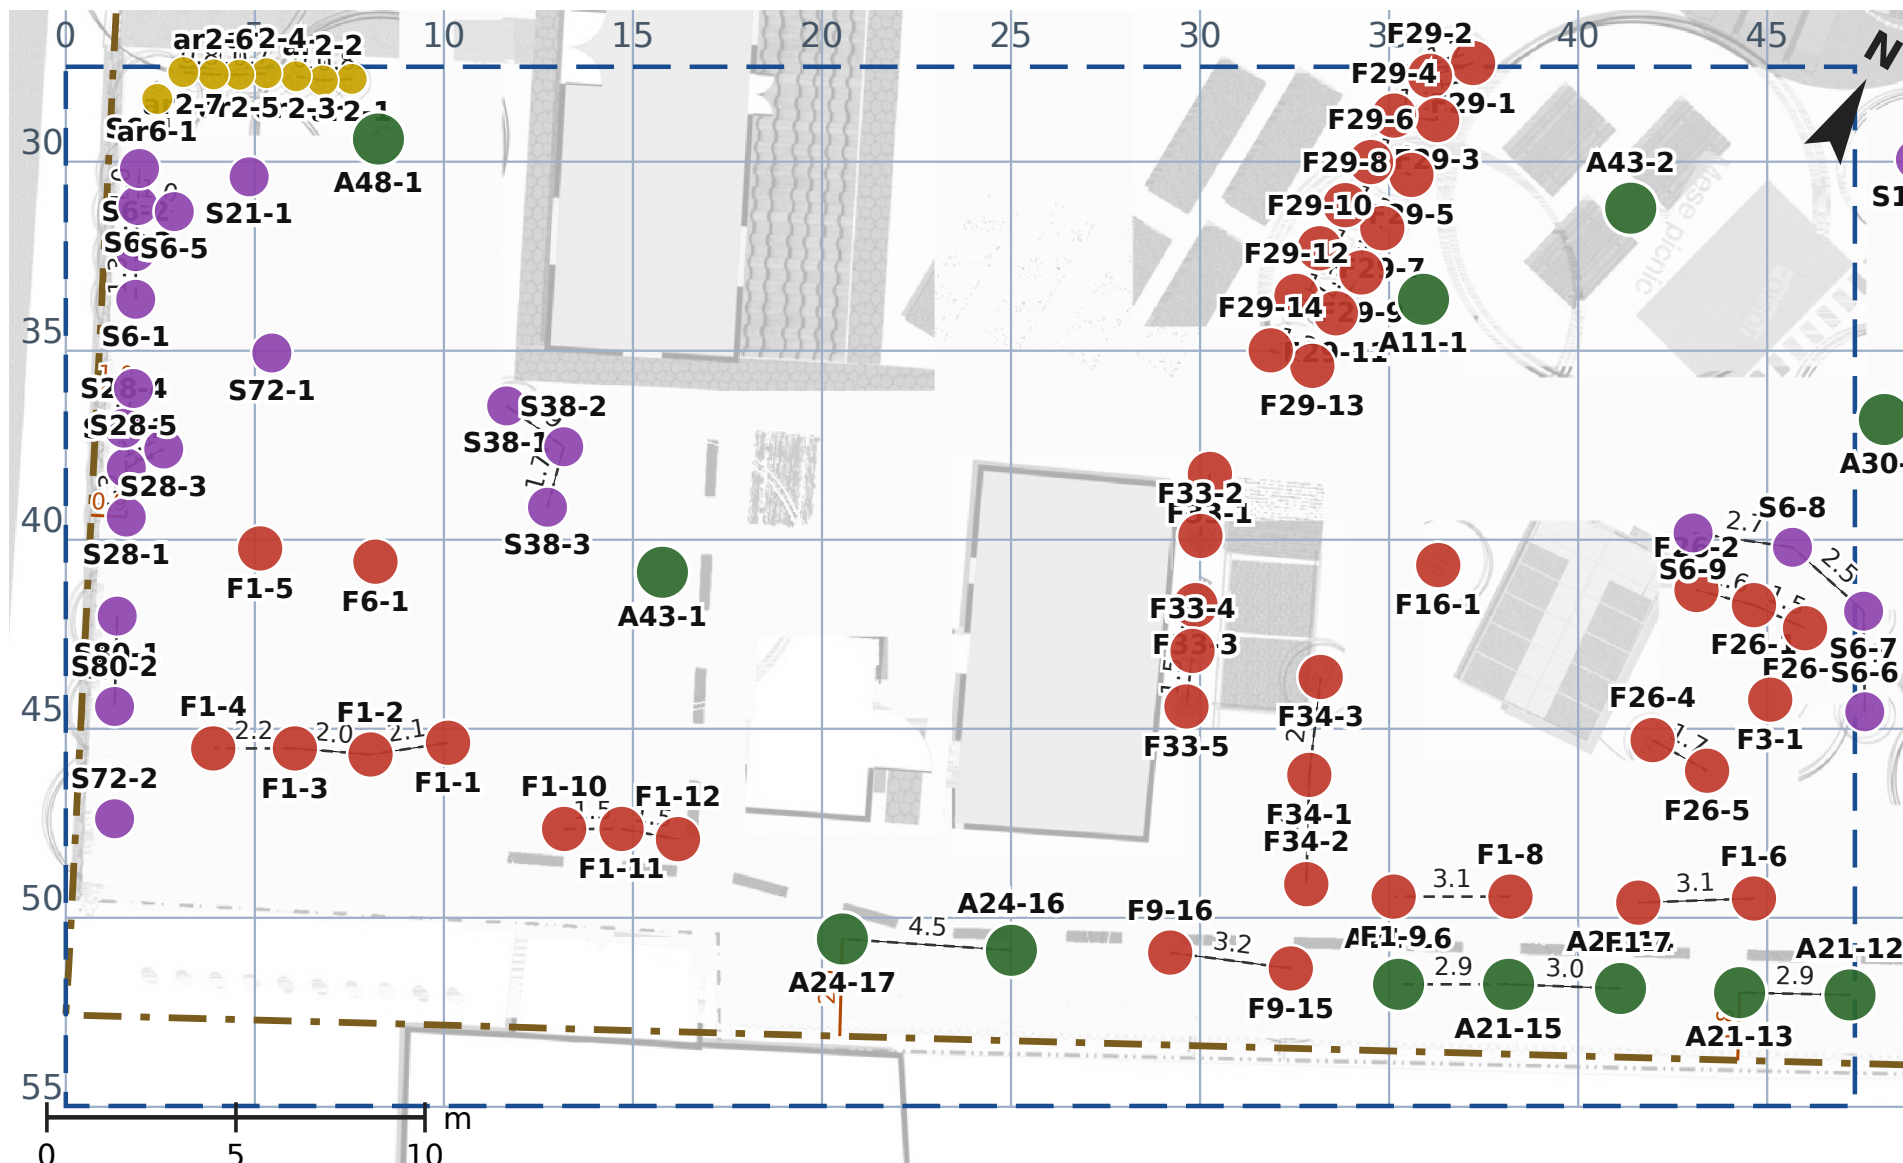


Cadran 4 — scara 1:200 (1 cm = 2 m)

88 plante în cadran. Eticheta = cod specie și număr (ex. A21-14). Linia punctată neagră cu cifră = distanța în metri până la cel mai apropiat exemplar din aceeași specie. Linia portocalie = distanța până la gard. Rețea de 5 m, coordonatele în metri ca pe foaia 1. Marginea suprapune 1,5 m peste cadranul vecin.

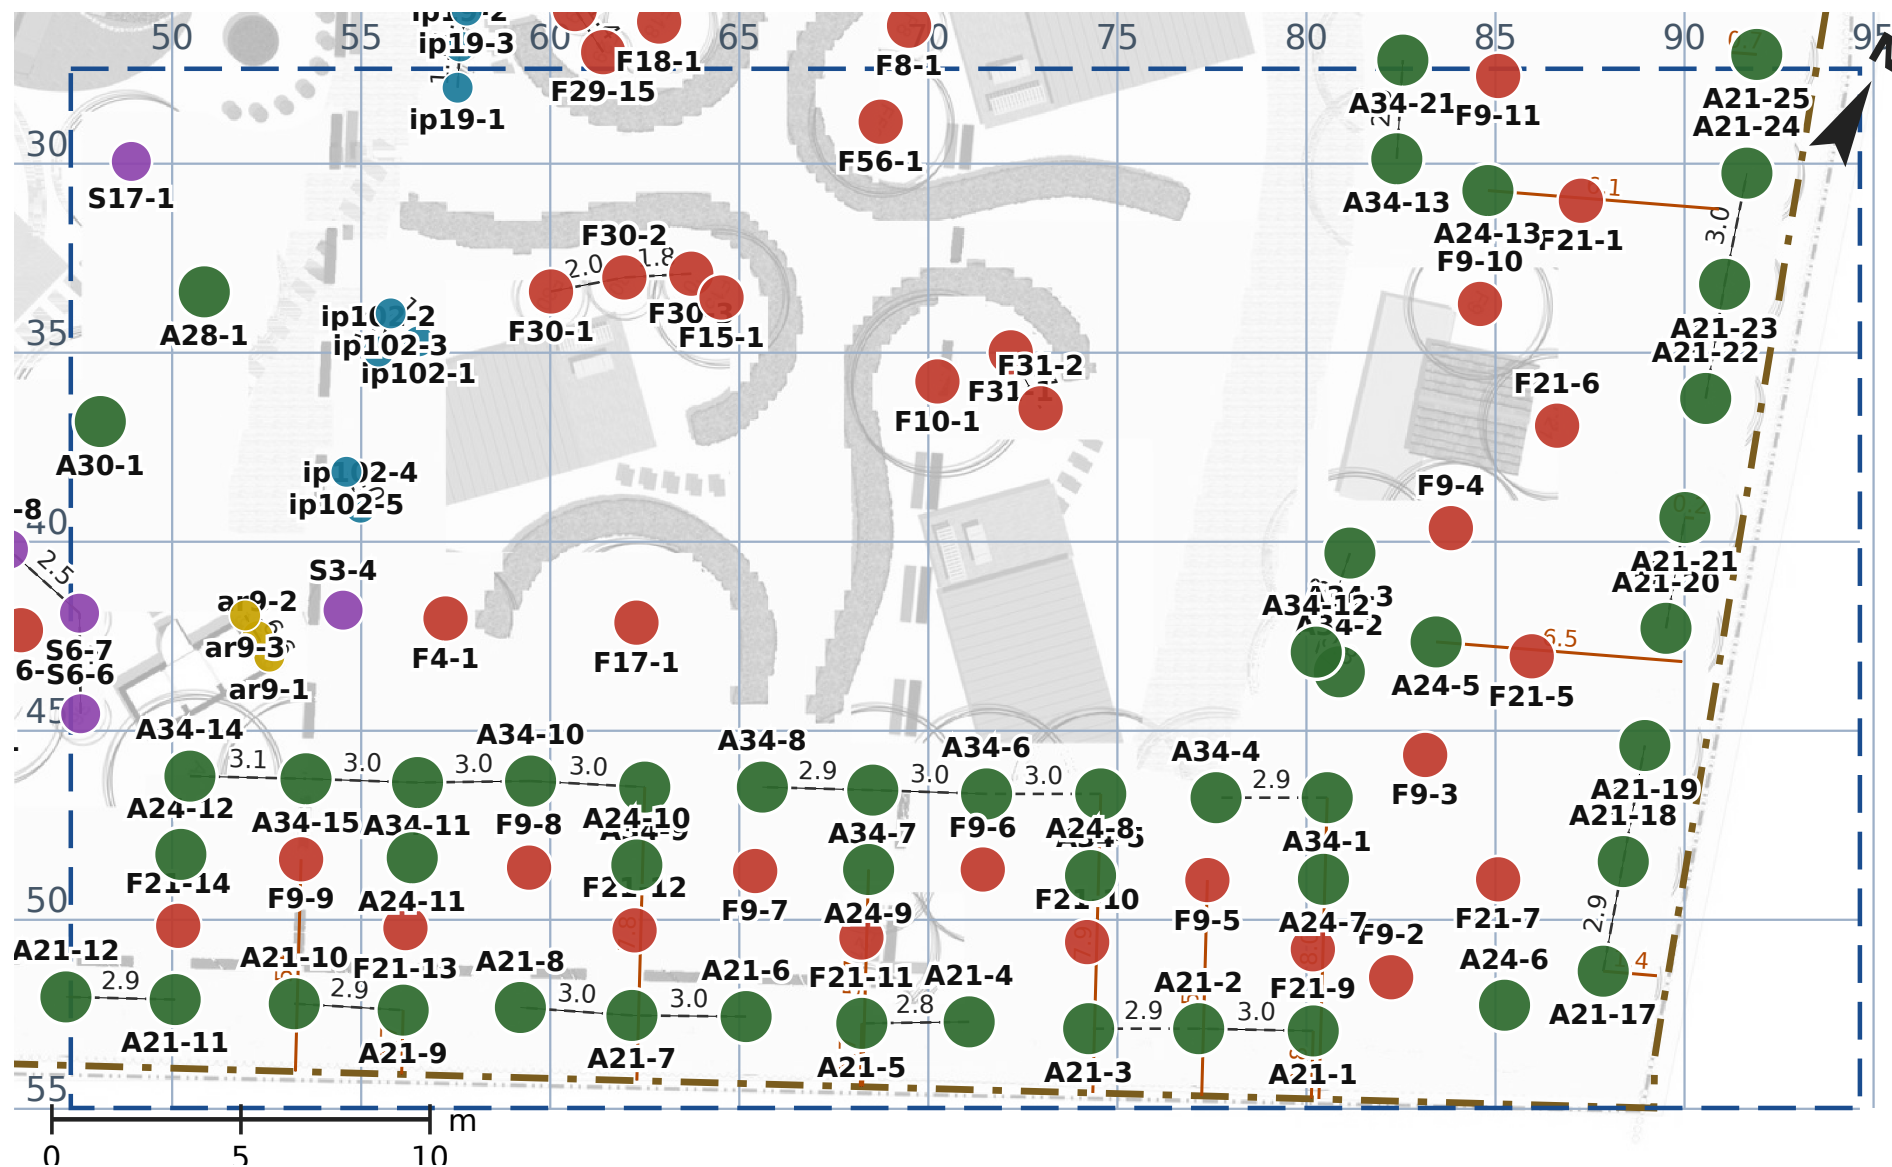

Perdeaua de nord — benzi desfășurate, scara ~1:150

Gardul de nord e linia de sus a fiecărei benzi; adâncimea (distanța de la gard, în metri) crește în jos, numerele portocalii de la gard sunt distanța fiecărei plante față de gard, numerele negre dintre două plante de aceeași specie sunt pasul pe rând. Rândul 1: ulm la 2 m de gard, din 2 în 2 m. Rândul 2: sălcioară la 3,75 m, din 3 în 3 m. Rândul 3: arbuștii existenți. Plante în bandă: Ulm de Turkestan 24, Sălcioară 15, Măceș 8, Păducel 7, Kerria 5, Ploaie de aur 4, Frasin 3, Aronia 3, Dud alb 2, Liliac de vară 2, Corn 1, Iasomie falsă 1, Pin negru 1, Pom de stafide 1, Prun 1, Soc 1, Vișin 1, Nuc 1, Călin 1.

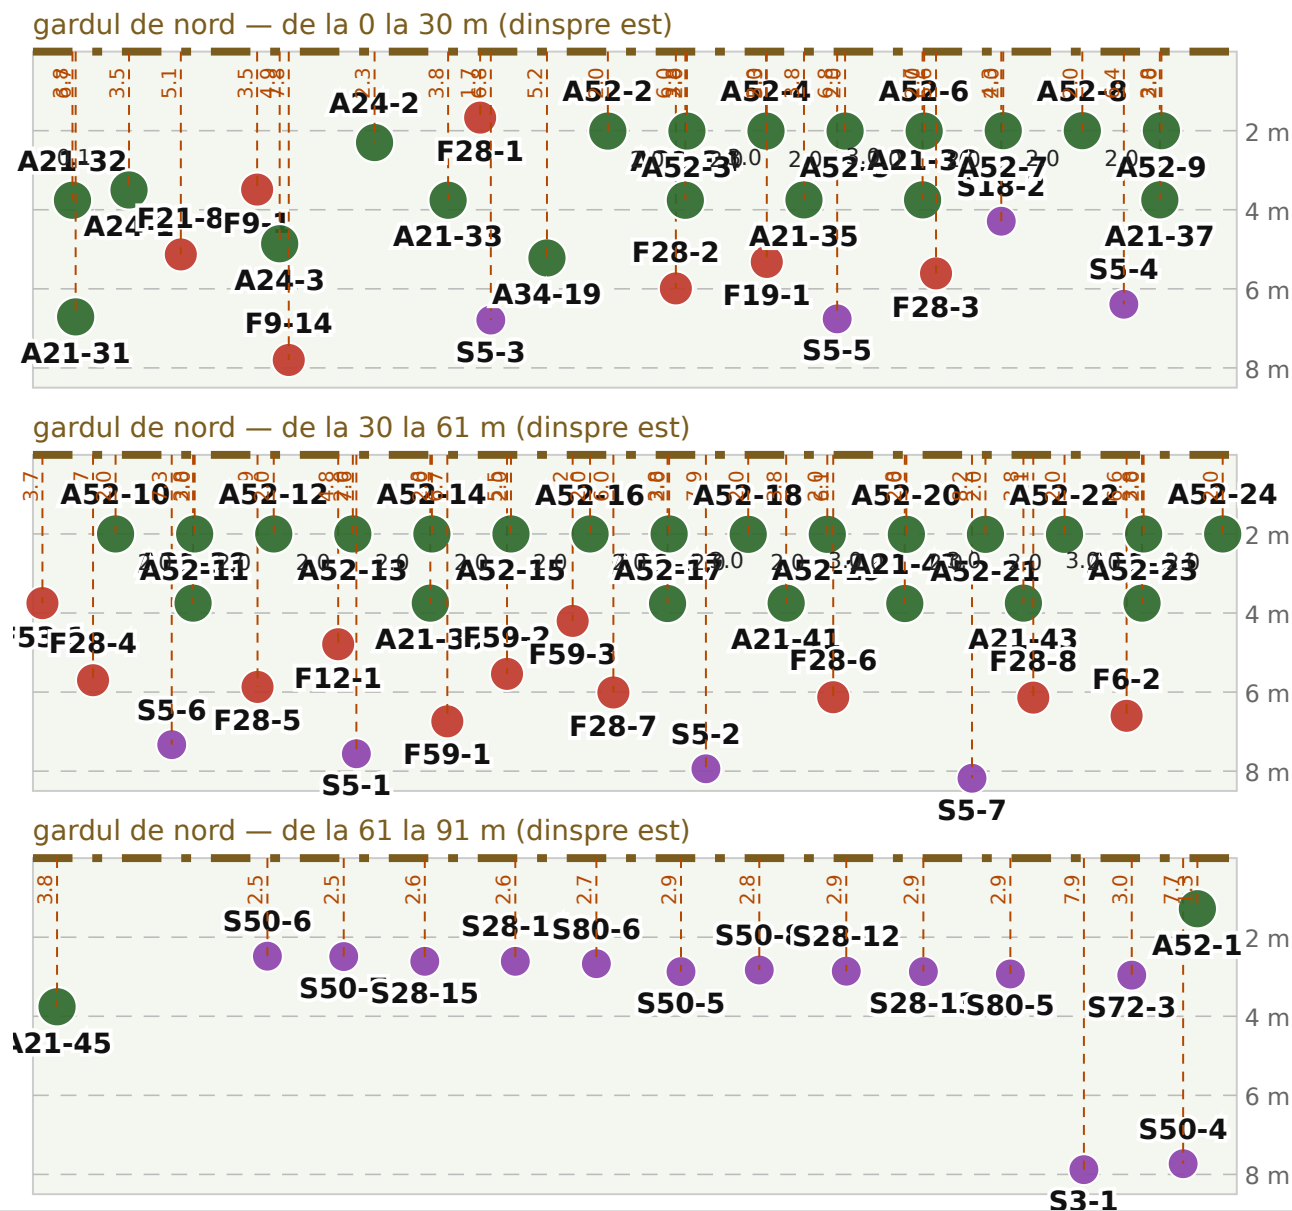

Legenda și lista speciilor

63 specii, 325 plante. Culoarea codului = tipul plantei (verde arbore, roșu fructifer, mov arbust, galben aromatică, albastru ierbacee); eticheta de pe foi = cod + numărul exemplarului. Distanța minimă e cea mai mică distanță dintre două exemplare din aceeași specie, așa cum sunt pe plan.

● Arbore 116 ● Fructifer 110 ● Arbust 66 ● Aromatică 17 ● Ierbacee 16

Cod	Specie	Buc.	Dist. min. (m)	Înălțime	Cadr.
A28	Arborele de lealea <i>Liriodendron tulipifera</i>	1	—	25–30 m	4
A11	Arborele de mătase <i>Albizia julibrissin</i>	1	—	6–9 m	3
A24	Frasin <i>Fraxinus excelsior</i>	17	3.5	25–30 m	2, 3, 4
A30	Magnolie <i>Magnolia × soulangiana</i>	1	—	6–8 m	4
A5	Paltin de câmp <i>Acer platanoides</i>	2	6.1	20–25 m	1
A34	Pin negru <i>Pinus nigra</i>	21	0.8	20–30 m	2, 4
A43	Salcie plângătoare <i>Salix babylonica</i>	2	27.4	10–12 m	3
A40	Stejar pufos <i>Quercus pubescens</i>	1	—	10–15 m	2
A21	Sălcioară <i>Elaeagnus angustifolia</i>	45	2.8	6–8 m	1, 2, 3, 4
A48	Tei argintiu <i>Tilia tomentosa</i>	1	—	25–30 m	3
A52	Ulm de Turkestan <i>Ulmus pumila</i>	24	2.0	12–15 m	1, 2
S38	Cununiță <i>Spiraea japonica</i>	3	1.7	1,2–1,5 m	3
S72	Călin <i>Viburnum opulus</i>	3	13.0	4–5 m	1, 3
S6	Hibiscus <i>Hibiscus syriacus</i>	9	1.0	3–4 m	3, 4
S3	Iasomie falsă <i>Philadelphus coronarius</i>	4	4.5	3,0 m	1, 4
S50	Kerria <i>Kerria japonica</i>	8	0.9	2,0–2,5 m	1
S21	Liliac <i>Syringa vulgaris</i>	2	46.4	4–5 m	2, 3
S80	Liliac de vară <i>Buddleja davidii</i>	6	2.0	2,5–3,0 m	1, 3
S17	Oțetar <i>Rhus typhina</i>	1	—	4–5 m	4
S28	Ploaie de aur <i>Forsythia × intermedia</i>	15	1.1	3,0 m	1, 3
S5	Păducel <i>Crataegus monogyna</i>	7	4.7	6–8 m	1, 2

Cod	Specie	Buc.	Dist. min. (m)	Înălțime	Cadr.
S10	Salcâm galben <i>Laburnum anagyroides</i>	1	—	5–7 m	1
S4	Scumpie <i>Cotinus coggygria</i>	1	—	4–5 m	2
S18	Soc <i>Sambucus nigra</i>	2	23.6	4–6 m	2
S69	Trandafir de Rescht <i>Rosa 'de Rescht'</i>	4	1.9	1,2–1,5 m	1
ar2	Lavandă <i>Lavandula angustifolia</i>	10	0.7	0,60–0,80 m	1, 3
ar9	Roiniță <i>Melissa officinalis</i>	3	0.6	0,80–1,00 m	4
ar6	Rozmarin <i>Salvia rosmarinus</i>	2	37.3	1,20–1,50 m	1, 3
ar7	Salvie <i>Salvia officinalis</i>	2	3.4	0,70–0,80 m	1
F32	Agriș <i>Ribes uva-crispa</i>	2	1.8	1,5 m	2
F1	Alun <i>Corylus avellana</i>	12	1.5	4–5 m	3
F34	Arbore de mazăre <i>Caragana arborescens</i>	3	2.6	4–6 m	3
F59	Aronia <i>Aronia melanocarpa</i>	3	1.9	2,0–2,5 m	2
F10	Cireș <i>Prunus avium</i>	1	—	6–9 m	4
F31	Coacăz alb <i>Ribes rubrum (varietatea albă)</i>	2	1.7	1,5 m	4
F30	Coacăz negru <i>Ribes nigrum</i>	3	1.8	1,8–2,0 m	4
F29	Coacăz roșu <i>Ribes rubrum</i>	16	1.1	1,5 m	1, 2, 3
F11	Corcoduș <i>Prunus cerasifera</i>	1	—	6–8 m	2
F21	Corn <i>Cornus mas</i>	14	5.2	5–6 m	2, 4
F26	Cătină <i>Hippophae rhamnoides</i>	5	1.5	4–6 m	3
F9	Dud alb <i>Morus alba</i>	16	3.2	10–12 m	2, 3, 4
F18	Jujuba <i>Ziziphus jujuba</i>	1	—	6–8 m	2

Cod	Specie	Buc.	Dist. min. (m)	Înălțime	Cadr.
F3	Kaki <i>Diospyros kaki</i>	2	34.1	6–8 m	2, 3
F14	Migdal <i>Prunus dulcis</i>	1	—	5–7 m	2
F8	Moșmon <i>Mespilus germanica</i>	1	—	4–6 m	2
F28	Măceș <i>Rosa canina</i>	8	4.2	3–4 m	1, 2
F7	Măr <i>Malus domestica</i>	1	—	4–5 m	1
F56	Nectarin <i>Prunus persica var. nucipersica</i>	1	—	4–5 m	4
F6	Nuc <i>Juglans regia</i>	2	42.8	15–20 m	1, 3
F15	Piersic <i>Prunus persica</i>	1	—	4–5 m	4
F19	Pom de stafide <i>Amelanchier lamarckii</i>	1	—	5–8 m	2
F53	Prun <i>Prunus domestica</i>	1	—	5–6 m	2
F17	Păr <i>Pyrus communis</i>	1	—	6–10 m	4
F16	Rodiu <i>Punica granatum</i>	1	—	3–4 m	3
F4	Smochin <i>Ficus carica</i>	2	29.7	4–6 m	2, 4
F44	Sânger <i>Cornus sanguinea</i>	2	2.0	4–5 m	2
F12	Vișin <i>Prunus cerasus</i>	1	—	4–5 m	2
F33	Viță de vie <i>Vitis vinifera</i>	5	1.2	2,0–2,5 m	3
ia19	Fenicul <i>Foeniculum vulgare</i>	2	1.3	2,00 m	2
ip44	Isop <i>Hyssopus officinalis</i>	2	3.5	0,60 m	1
ip102	Lofantus <i>Agastache foeniculum</i>	5	1.0	1,20 m	4
ip126	Potentilla <i>Potentilla fruticosa</i>	3	1.0	1,00–1,20 m	2
ip19	Tătăneasă <i>Symphytum officinale</i>	4	1.0	1,20 m	2, 4

Tabel de trasare (1-126 din 325)

C = cadran. x, y = metri de la originea din foaia 1 (stânga-sus; x spre dreapta, y în jos). d1, d2 = distanța perpendiculară (m) până la cele mai apropiate două garduri (N = nord, S = sud, E = est, V = vest, adică strada) — se măsoară cu ruleta, perpendicular pe gard. Ordonat pe cadran, specie, număr.

C	Plantă	Specie	x	y	d1	de la	d2	de la
1	A21-40	Sălcioară	46.8	4.8	3.8	gard N	44.4	gard V
1	A21-41	Sălcioară	43.8	4.7	3.8	gard N	41.4	gard V
1	A21-42	Sălcioară	40.8	4.6	3.8	gard N	38.4	gard V
1	A21-43	Sălcioară	37.8	4.6	3.8	gard N	35.4	gard V
1	A21-44	Sălcioară	34.8	4.5	3.8	gard N	32.4	gard V
1	A21-45	Sălcioară	31.8	4.4	3.8	gard N	29.4	gard V
1	A5-1	Paltin de câmp	20.4	11.3	10.9	gard N	18.3	gard V
1	A5-2	Paltin de câmp	24.0	16.2	15.7	gard N	22.2	gard V
1	A52-1	Ulm de Turkestan	3.0	1.3	0.5	gard V	1.3	gard N
1	A52-17	Ulm de Turkestan	46.8	3.0	2.0	gard N	44.3	gard V
1	A52-18	Ulm de Turkestan	44.8	3.0	2.0	gard N	42.3	gard V
1	A52-19	Ulm de Turkestan	42.8	2.9	2.0	gard N	40.3	gard V
1	A52-20	Ulm de Turkestan	40.8	2.9	2.0	gard N	38.3	gard V
1	A52-21	Ulm de Turkestan	38.8	2.8	2.0	gard N	36.3	gard V
1	A52-22	Ulm de Turkestan	36.8	2.8	2.0	gard N	34.3	gard V
1	A52-23	Ulm de Turkestan	34.8	2.7	2.0	gard N	32.3	gard V
1	A52-24	Ulm de Turkestan	32.8	2.7	2.0	gard N	30.3	gard V
1	F28-6	Măceș	42.6	7.0	6.1	gard N	40.2	gard V
1	F28-8	Măceș	37.5	6.9	6.1	gard N	35.2	gard V
1	F29-1	Coacăz roșu	37.2	27.4	26.2	gard S	26.6	gard N
1	F6-2	Nuc	35.1	7.4	6.6	gard N	32.8	gard V
1	F7-1	Măr	18.9	19.0	17.2	gard V	18.6	gard N
1	S10-1	Salcâm galben	9.3	23.2	7.8	gard V	23.0	gard N
1	S28-6	Ploaie de aur	2.5	17.8	0.7	gard V	17.7	gard N
1	S28-7	Ploaie de aur	2.3	18.9	0.6	gard V	18.8	gard N
1	S28-8	Ploaie de aur	3.4	19.5	1.7	gard V	19.4	gard N
1	S28-9	Ploaie de aur	2.3	19.9	0.7	gard V	19.9	gard N
1	S28-10	Ploaie de aur	2.1	21.1	0.5	gard V	21.1	gard N
1	S28-11	Ploaie de aur	2.0	22.3	0.5	gard V	22.2	gard N
1	S28-12	Ploaie de aur	11.9	3.1	2.9	gard N	9.4	gard V
1	S28-13	Ploaie de aur	9.9	3.1	2.9	gard N	7.4	gard V
1	S28-14	Ploaie de aur	20.2	3.0	2.6	gard N	17.7	gard V
1	S28-15	Ploaie de aur	22.5	3.1	2.6	gard N	20.0	gard V
1	S3-1	lasomie falsă	5.8	8.0	3.5	gard V	7.9	gard N
1	S3-2	lasomie falsă	29.3	17.5	16.8	gard N	27.5	gard V
1	S3-3	lasomie falsă	31.7	13.6	13.0	gard N	29.8	gard V
1	S5-2	Păducel	45.7	8.9	7.9	gard N	43.5	gard V
1	S5-7	Păducel	39.0	9.0	8.2	gard N	36.8	gard V
1	S50-1	Kerria	2.8	10.9	0.7	gard V	10.8	gard N
1	S50-2	Kerria	2.9	9.7	0.8	gard V	9.6	gard N
1	S50-3	Kerria	3.1	8.7	0.9	gard V	8.7	gard N
1	S50-4	Kerria	3.2	7.8	1.0	gard V	7.7	gard N

C	Plantă	Specie	x	y	d1	de la	d2	de la
1	S50-5	Kerria	16.0	3.2	2.9	gard N	13.6	gard V
1	S50-6	Kerria	26.5	3.0	2.5	gard N	24.0	gard V
1	S50-7	Kerria	24.6	3.0	2.5	gard N	22.1	gard V
1	S50-8	Kerria	14.1	3.1	2.8	gard N	11.6	gard V
1	S69-1	Trandafir de Rescht	23.3	20.0	19.5	gard N	21.6	gard V
1	S69-2	Trandafir de Rescht	23.4	18.1	17.6	gard N	21.7	gard V
1	S69-3	Trandafir de Rescht	25.5	17.0	16.4	gard N	23.7	gard V
1	S69-4	Trandafir de Rescht	27.7	17.2	16.6	gard N	25.9	gard V
1	S72-3	Călin	4.6	3.1	2.2	gard V	3.0	gard N
1	S80-3	Liliac de vară	2.9	13.5	0.9	gard V	13.4	gard N
1	S80-4	Liliac de vară	2.8	15.5	0.9	gard V	15.4	gard N
1	S80-5	Liliac de vară	7.7	3.1	2.9	gard N	5.2	gard V
1	S80-6	Liliac de vară	18.2	3.1	2.7	gard N	15.7	gard V
1	ar2-8	Lavandă	38.0	21.5	20.7	gard N	32.0	gard S
1	ar2-9	Lavandă	38.6	18.2	17.4	gard N	35.4	gard S
1	ar2-10	Lavandă	40.8	15.5	14.6	gard N	38.1	gard S
1	ar6-2	Rozmarin	39.1	21.9	21.0	gard N	31.8	gard S
1	ar7-1	Salvie	38.3	19.3	18.5	gard N	34.3	gard S
1	ar7-2	Salvie	39.9	16.3	15.4	gard N	37.3	gard S
1	ip44-1	Isop	38.2	20.5	19.7	gard N	33.1	gard S
1	ip44-2	Isop	39.2	17.2	16.3	gard N	36.4	gard S
2	A21-25	Sălcioară	91.9	27.1	0.7	gard E	25.2	gard N
2	A21-26	Sălcioară	92.0	24.0	0.5	gard E	22.0	gard N
2	A21-27	Sălcioară	92.0	21.0	0.3	gard E	19.0	gard N
2	A21-28	Sălcioară	92.1	17.9	0.1	gard E	16.0	gard N
2	A21-29	Sălcioară	92.0	14.8	0.2	gard E	12.9	gard N
2	A21-30	Sălcioară	92.1	11.8	0.4	gard E	9.8	gard N
2	A21-31	Sălcioară	92.2	8.7	0.6	gard E	6.7	gard N
2	A21-32	Sălcioară	92.3	5.7	0.7	gard E	3.8	gard N
2	A21-33	Sălcioară	82.8	5.5	3.8	gard N	10.2	gard E
2	A21-34	Sălcioară	76.8	5.4	3.8	gard N	16.1	gard E
2	A21-35	Sălcioară	73.8	5.3	3.8	gard N	19.1	gard E
2	A21-36	Sălcioară	70.8	5.3	3.7	gard N	22.1	gard E
2	A21-37	Sălcioară	64.8	5.1	3.8	gard N	28.1	gard E
2	A21-38	Sălcioară	58.8	5.0	3.8	gard N	34.1	gard E
2	A21-39	Sălcioară	52.8	4.9	3.8	gard N	40.1	gard E
2	A24-1	Frasin	90.9	5.4	2.1	gard E	3.5	gard N
2	A24-2	Frasin	84.7	4.1	2.3	gard N	8.4	gard E
2	A24-3	Frasin	87.0	6.7	4.9	gard N	5.8	gard E
2	A24-4	Frasin	86.5	12.8	5.9	gard E	10.9	gard N
2	A24-14	Frasin	85.4	24.7	6.0	gard E	22.8	gard N
2	A24-15	Frasin	86.0	18.7	5.9	gard E	16.9	gard N

C	Plantă	Specie	x	y	d1	de la	d2	de la
2	A34-16	Pin negru	83.7	15.3	8.5	gard E	13.5	gard N
2	A34-17	Pin negru	83.4	18.3	8.5	gard E	16.5	gard N
2	A34-18	Pin negru	83.2	21.4	8.5	gard E	19.6	gard N
2	A34-19	Pin negru	80.3	6.9	5.2	gard N	12.6	gard E
2	A34-20	Pin negru	82.8	24.3	8.7	gard E	22.5	gard N
2	A34-21	Pin negru	82.5	27.3	8.7	gard E	25.5	gard N
2	A40-1	Stejar pufos	84.4	10.4	8.2	gard E	8.6	gard N
2	A52-2	Ulm de Turkestan	78.8	3.7	2.0	gard N	14.3	gard E
2	A52-3	Ulm de Turkestan	76.8	3.6	2.0	gard N	16.3	gard E
2	A52-4	Ulm de Turkestan	74.8	3.6	2.0	gard N	18.3	gard E
2	A52-5	Ulm de Turkestan	72.8	3.6	2.0	gard N	20.3	gard E
2	A52-6	Ulm de Turkestan	70.8	3.5	2.0	gard N	22.3	gard E
2	A52-7	Ulm de Turkestan	68.8	3.5	2.0	gard N	24.3	gard E
2	A52-8	Ulm de Turkestan	66.8	3.4	2.0	gard N	26.3	gard E
2	A52-9	Ulm de Turkestan	64.8	3.4	2.0	gard N	28.3	gard E
2	A52-10	Ulm de Turkestan	60.8	3.3	2.0	gard N	32.3	gard E
2	A52-11	Ulm de Turkestan	58.8	3.3	2.0	gard N	34.3	gard E
2	A52-12	Ulm de Turkestan	56.8	3.2	2.0	gard N	36.3	gard E
2	A52-13	Ulm de Turkestan	54.8	3.2	2.0	gard N	38.3	gard E
2	A52-14	Ulm de Turkestan	52.8	3.1	2.0	gard N	40.2	gard E
2	A52-15	Ulm de Turkestan	50.8	3.1	2.0	gard N	42.2	gard E
2	A52-16	Ulm de Turkestan	48.8	3.0	2.0	gard N	44.2	gard E
2	F11-1	Corcoduș	54.9	14.7	13.5	gard N	37.2	gard E
2	F12-1	Vișin	55.1	6.0	4.8	gard N	37.7	gard E
2	F14-1	Migdal	69.9	19.4	18.0	gard N	21.9	gard E
2	F18-1	Jujuba	62.9	26.2	24.9	gard N	28.0	gard S
2	F19-1	Pom de stafide	74.7	6.9	5.3	gard N	18.1	gard E
2	F21-2	Corn	87.8	25.0	3.6	gard E	23.1	gard N
2	F21-3	Corn	88.4	19.0	3.5	gard E	17.1	gard N
2	F21-4	Corn	89.0	13.0	3.4	gard E	11.1	gard N
2	F21-8	Corn	89.5	7.0	3.3	gard E	5.1	gard N
2	F28-1	Măceș	82.0	3.4	1.7	gard N	11.1	gard E
2	F28-2	Măceș	77.0	7.6	6.0	gard N	15.8	gard E
2	F28-3	Măceș	70.4	7.1	5.6	gard N	22.4	gard E
2	F28-4	Măceș	61.3	7.0	5.7	gard N	31.5	gard E
2	F28-5	Măceș	57.1	7.1	5.9	gard N	35.6	gard E
2	F28-7	Măceș	48.1	7.0	6.0	gard N	44.6	gard E
2	F29-15	Coacăz roșu	61.4	27.0	25.7	gard N	27.2	gard S
2	F29-16	Coacăz roșu	60.6	25.9	24.6	gard N	28.3	gard S
2	F3-2	Kaki	60.0	13.5	12.2	gard N	32.3	gard E
2	F32-1	Agriș	71.8	20.7	19.2	gard N	19.9	gard E
2	F32-2	Agriș	70.0	21.0	19.5	gard N	21.7	gard E

Tabel de trasare (127-252 din 325)

C = cadran. x, y = metri de la originea din foaia 1 (stânga-sus; x spre dreapta, y în jos). d1, d2 = distanța perpendiculară (m) până la cele mai apropiate două garduri (N = nord, S = sud, E = est, V = vest, adică strada) — se măsoară cu ruleta, perpendicular pe gard. Ordonat pe cadran, specie, număr.

C	Plantă	Specie	x	y	d1	de la	d2	de la
2	F4-2	Smochin	65.2	13.4	12.0	gard N	27.1	gard E
2	F44-1	Sânger	56.9	18.7	17.5	gard N	34.9	gard E
2	F44-2	Sânger	57.6	20.5	19.3	gard N	33.6	gard S
2	F53-1	Prun	62.6	5.1	3.7	gard N	30.3	gard E
2	F59-1	Aronia	52.3	7.9	6.7	gard N	40.4	gard E
2	F59-2	Aronia	50.8	6.6	5.5	gard N	41.9	gard E
2	F59-3	Aronia	49.2	5.2	4.2	gard N	43.7	gard E
2	F8-1	Moșmon	69.5	26.3	21.7	gard E	24.9	gard N
2	F9-1	Dud alb	87.6	5.4	3.5	gard N	5.4	gard E
2	F9-12	Dud alb	85.6	21.7	6.0	gard E	19.9	gard N
2	F9-13	Dud alb	86.2	15.7	6.0	gard E	13.8	gard N
2	F9-14	Dud alb	86.7	9.6	5.9	gard E	7.8	gard N
2	S18-1	Soc	53.3	23.6	22.5	gard N	30.4	gard S
2	S18-2	Soc	68.8	5.8	4.3	gard N	24.1	gard E
2	S21-2	Liliac	49.0	16.1	15.1	gard N	37.8	gard S
2	S4-1	Scumpie	58.6	23.2	22.0	gard N	30.9	gard S
2	S5-1	Păducel	54.6	8.7	7.6	gard N	38.0	gard E
2	S5-3	Păducel	81.7	8.5	6.8	gard N	11.1	gard E
2	S5-4	Păducel	65.7	7.8	6.4	gard N	27.1	gard E
2	S5-5	Păducel	72.9	8.3	6.8	gard N	19.8	gard E
2	S5-6	Păducel	59.3	8.6	7.3	gard N	33.4	gard E
2	ia19-1	Fenicul	53.0	22.4	21.3	gard N	31.6	gard S
2	ia19-2	Fenicul	52.8	21.2	20.0	gard N	32.8	gard S
2	ip126-1	Potentilla	51.1	18.3	17.2	gard N	35.7	gard S
2	ip126-2	Potentilla	51.7	19.1	18.0	gard N	34.9	gard S
2	ip126-3	Potentilla	52.2	20.0	18.9	gard N	33.9	gard S
2	ip19-2	Tătăneasă	57.6	26.9	25.7	gard N	27.2	gard S
2	ip19-3	Tătăneasă	57.8	26.0	24.7	gard N	28.2	gard S
2	ip19-4	Tătăneasă	57.9	24.9	23.7	gard N	29.2	gard S
3	A11-1	Arborele de mătase	35.9	33.6	19.9	gard S	32.9	gard N
3	A21-12	Sălcioară	47.2	52.0	1.8	gard S	41.9	gard E
3	A21-13	Sălcioară	44.3	52.0	1.8	gard S	44.2	gard V
3	A21-14	Sălcioară	41.1	51.9	1.8	gard S	41.0	gard V
3	A21-15	Sălcioară	38.2	51.8	1.8	gard S	38.1	gard V
3	A21-16	Sălcioară	35.2	51.8	1.8	gard S	35.1	gard V
3	A24-16	Frasin	25.0	50.9	2.4	gard S	24.9	gard V
3	A24-17	Frasin	20.5	50.6	2.6	gard S	20.4	gard V
3	A43-1	Salcie plângătoare	15.8	40.9	12.1	gard S	15.2	gard V
3	A43-2	Salcie plângătoare	41.4	31.2	22.5	gard S	30.3	gard N
3	A48-1	Tei argintiu	8.3	29.4	7.1	gard V	23.4	gard S
3	F1-1	Alun	10.1	45.4	7.5	gard S	9.7	gard V
3	F1-2	Alun	8.1	45.7	7.1	gard S	7.7	gard V

C	Plantă	Specie	x	y	d1	de la	d2	de la
3	F1-3	Alun	6.1	45.5	5.7	gard V	7.2	gard S
3	F1-4	Alun	3.9	45.5	3.5	gard V	7.2	gard S
3	F1-5	Alun	5.1	40.2	4.5	gard V	12.5	gard S
3	F1-6	Alun	44.7	49.5	4.3	gard S	44.4	gard V
3	F1-7	Alun	41.6	49.6	4.1	gard S	41.4	gard V
3	F1-8	Alun	38.2	49.4	4.2	gard S	38.0	gard V
3	F1-9	Alun	35.1	49.4	4.1	gard S	34.9	gard V
3	F1-10	Alun	13.2	47.6	5.3	gard S	12.9	gard V
3	F1-11	Alun	14.7	47.6	5.3	gard S	14.4	gard V
3	F1-12	Alun	16.2	47.9	5.1	gard S	15.9	gard V
3	F16-1	Rodiu	36.3	40.7	12.9	gard S	35.6	gard V
3	F26-1	Cătină	44.7	41.7	12.0	gard S	40.8	gard N
3	F26-2	Cătină	43.1	41.3	12.4	gard S	40.4	gard N
3	F26-3	Cătină	46.0	42.3	11.5	gard S	41.4	gard N
3	F26-4	Cătină	42.0	45.3	8.4	gard S	41.5	gard V
3	F26-5	Cătină	43.4	46.1	7.6	gard S	43.0	gard V
3	F29-2	Coacăz roșu	36.1	27.7	25.8	gard S	27.0	gard N
3	F29-3	Coacăz roșu	36.3	28.9	24.6	gard S	28.1	gard N
3	F29-4	Coacăz roșu	35.1	28.8	24.7	gard S	28.0	gard N
3	F29-5	Coacăz roșu	35.6	30.3	23.2	gard S	29.6	gard N
3	F29-6	Coacăz roșu	34.5	30.0	23.5	gard S	29.3	gard N
3	F29-7	Coacăz roșu	34.8	31.8	21.7	gard S	31.0	gard N
3	F29-8	Coacăz roșu	33.8	31.1	22.3	gard S	30.4	gard N
3	F29-9	Coacăz roșu	34.3	32.9	20.6	gard S	32.2	gard N
3	F29-10	Coacăz roșu	33.2	32.3	21.2	gard S	31.6	gard N
3	F29-11	Coacăz roșu	33.6	34.0	19.5	gard S	32.6	gard V
3	F29-12	Coacăz roșu	32.5	33.6	19.9	gard S	31.5	gard V
3	F29-13	Coacăz roșu	33.0	35.4	18.1	gard S	32.1	gard V
3	F29-14	Coacăz roșu	31.9	35.0	18.4	gard S	30.9	gard V
3	F3-1	Kaki	45.1	44.2	9.6	gard S	43.3	gard N
3	F33-1	Viță de vie	30.3	38.3	15.1	gard S	29.5	gard V
3	F33-2	Viță de vie	30.0	39.9	13.5	gard S	29.3	gard V
3	F33-3	Viță de vie	29.9	41.7	11.6	gard S	29.3	gard V
3	F33-4	Viță de vie	29.8	42.9	10.4	gard S	29.3	gard V
3	F33-5	Viță de vie	29.6	44.4	9.0	gard S	29.2	gard V
3	F34-1	Arbore de mazăre	32.9	46.2	7.2	gard S	32.5	gard V
3	F34-2	Arbore de mazăre	32.8	49.1	4.3	gard S	32.6	gard V
3	F34-3	Arbore de mazăre	33.2	43.6	9.8	gard S	32.7	gard V
3	F6-1	Nuc	8.2	40.6	7.6	gard V	12.2	gard S
3	F9-15	Dud alb	32.4	51.3	2.1	gard S	32.3	gard V
3	F9-16	Dud alb	29.2	50.9	2.4	gard S	29.1	gard V
3	S21-1	Liliac	4.9	30.4	3.7	gard V	22.3	gard S

C	Plantă	Specie	x	y	d1	de la	d2	de la
3	S28-1	Ploaie de aur	1.6	39.4	0.9	gard V	13.2	gard S
3	S28-2	Ploaie de aur	1.6	38.1	0.9	gard V	14.5	gard S
3	S28-3	Ploaie de aur	2.6	37.6	1.8	gard V	15.0	gard S
3	S28-4	Ploaie de aur	1.5	37.0	0.8	gard V	15.6	gard S
3	S28-5	Ploaie de aur	1.8	36.0	1.0	gard V	16.6	gard S
3	S38-1	Cununiță	11.7	36.5	10.8	gard V	16.4	gard S
3	S38-2	Cununiță	13.2	37.5	12.4	gard V	15.4	gard S
3	S38-3	Cununiță	12.7	39.1	12.0	gard V	13.8	gard S
3	S6-1	Hibiscus	1.9	33.6	0.9	gard V	19.0	gard S
3	S6-2	Hibiscus	1.9	32.4	0.8	gard V	20.2	gard S
3	S6-3	Hibiscus	1.9	31.2	0.8	gard V	21.5	gard S
3	S6-4	Hibiscus	1.9	30.2	0.8	gard V	22.4	gard S
3	S6-5	Hibiscus	2.9	31.3	1.8	gard V	21.3	gard S
3	S6-8	Hibiscus	45.7	40.2	13.6	gard S	39.2	gard N
3	S6-9	Hibiscus	43.0	39.8	13.9	gard S	38.9	gard N
3	S72-1	Călin	5.4	35.1	4.6	gard V	17.7	gard S
3	S72-2	Călin	1.3	47.4	1.0	gard V	5.2	gard S
3	S80-1	Liliac de vară	1.4	42.0	0.8	gard V	10.6	gard S
3	S80-2	Liliac de vară	1.3	44.4	0.9	gard V	8.2	gard S
3	ar2-1	Lavandă	7.6	27.8	6.3	gard V	25.0	gard S
3	ar2-2	Lavandă	6.8	27.9	5.6	gard V	24.9	gard S
3	ar2-3	Lavandă	6.1	27.7	4.8	gard V	25.0	gard S
3	ar2-4	Lavandă	5.3	27.7	4.1	gard V	25.0	gard S
3	ar2-5	Lavandă	4.6	27.7	3.3	gard V	25.0	gard S
3	ar2-6	Lavandă	3.9	27.7	2.7	gard V	25.0	gard S
3	ar2-7	Lavandă	3.1	27.6	1.9	gard V	25.0	gard S
3	ar6-1	Rozmarin	2.4	28.3	1.2	gard V	24.3	gard S
4	A21-1	Sălcioară	80.2	52.9	1.8	gard S	8.9	gard E
4	A21-2	Sălcioară	77.2	52.9	1.8	gard S	12.0	gard E
4	A21-3	Sălcioară	74.2	52.9	1.7	gard S	14.9	gard E
4	A21-4	Sălcioară	71.1	52.7	1.8	gard S	18.0	gard E
4	A21-5	Sălcioară	68.2	52.7	1.7	gard S	20.9	gard E
4	A21-6	Sălcioară	65.2	52.6	1.8	gard S	23.9	gard E
4	A21-7	Sălcioară	62.2	52.5	1.7	gard S	26.9	gard E
4	A21-8	Sălcioară	59.2	52.3	1.8	gard S	29.9	gard E
4	A21-9	Sălcioară	56.1	52.4	1.7	gard S	33.0	gard E
4	A21-10	Sălcioară	53.2	52.2	1.8	gard S	35.9	gard E
4	A21-11	Sălcioară	50.1	52.1	1.8	gard S	39.0	gard E
4	A21-17	Sălcioară	87.9	51.4	1.4	gard E	3.6	gard S
4	A21-18	Sălcioară	88.4	48.5	1.1	gard E	6.5	gard S
4	A21-19	Sălcioară	88.9	45.4	0.8	gard E	9.6	gard S
4	A21-20	Sălcioară	89.5	42.3	0.5	gard E	12.7	gard S

Tabel de trasare (253-325 din 325)

C = cadran. x, y = metri de la originea din foaia 1 (stânga-sus; x spre dreapta, y în jos). d1, d2 = distanța perpendiculară (m) până la cele mai apropiate două garduri (N = nord, S = sud, E = est, V = vest, adică strada) — se măsoară cu ruleta, perpendicular pe gard. Ordonat pe cadran, specie, număr.

C	Plantă	Specie	x	y	d1	de la	d2	de la	C	Plantă	Specie	x	y	d1	de la	d2	de la
4	A21-21	Sălcioară	90.0	39.4	0.2	gard E	15.6	gard S	4	F21-14	Corn	50.2	50.2	3.8	gard S	39.1	gard E
4	A21-22	Sălcioară	90.6	36.2	0.0	gard E	18.8	gard S	4	F30-1	Coacăz negru	60.0	33.4	20.8	gard S	30.6	gard E
4	A21-23	Sălcioară	91.1	33.2	0.3	gard E	21.8	gard S	4	F30-2	Coacăz negru	62.0	33.0	21.2	gard S	28.7	gard E
4	A21-24	Sălcioară	91.7	30.3	0.7	gard E	24.8	gard S	4	F30-3	Coacăz negru	63.7	32.9	21.4	gard S	27.0	gard E
4	A24-5	Frasin	83.4	42.6	6.5	gard E	12.2	gard S	4	F31-1	Coacăz alb	72.2	35.0	18.4	gard E	19.5	gard S
4	A24-6	Frasin	85.2	52.3	2.6	gard S	4.0	gard E	4	F31-2	Coacăz alb	73.0	36.5	17.5	gard E	18.1	gard S
4	A24-7	Frasin	80.5	48.9	5.8	gard S	9.0	gard E	4	F4-1	Smochin	57.2	42.0	12.1	gard S	32.7	gard E
4	A24-8	Frasin	74.3	48.8	5.7	gard S	15.2	gard E	4	F56-1	Nectarin	68.7	28.9	22.3	gard E	25.5	gard S
4	A24-9	Frasin	68.4	48.7	5.7	gard S	21.0	gard E	4	F9-2	Dud alb	82.2	51.5	3.3	gard S	7.0	gard E
4	A24-10	Frasin	62.3	48.5	5.7	gard S	27.1	gard E	4	F9-3	Dud alb	83.1	45.6	6.6	gard E	9.2	gard S
4	A24-11	Frasin	56.4	48.4	5.7	gard S	33.1	gard E	4	F9-4	Dud alb	83.8	39.6	6.4	gard E	15.2	gard S
4	A24-12	Frasin	50.2	48.3	5.7	gard S	39.2	gard E	4	F9-5	Dud alb	77.4	49.0	5.7	gard S	12.1	gard E
4	A24-13	Frasin	84.8	30.7	6.1	gard E	24.1	gard S	4	F9-6	Dud alb	71.4	48.7	5.8	gard S	18.0	gard E
4	A28-1	Arborele de lea	50.9	33.4	20.5	gard S	32.3	gard N	4	F9-7	Dud alb	65.4	48.7	5.6	gard S	24.0	gard E
4	A30-1	Magnolie	48.1	36.8	17.0	gard S	35.8	gard N	4	F9-8	Dud alb	59.4	48.6	5.6	gard S	30.0	gard E
4	A34-1	Pin negru	80.5	46.8	8.0	gard S	9.1	gard E	4	F9-9	Dud alb	53.4	48.4	5.6	gard S	36.0	gard E
4	A34-2	Pin negru	80.9	43.4	9.0	gard E	11.3	gard S	4	F9-10	Dud alb	84.6	33.7	6.1	gard E	21.1	gard S
4	A34-3	Pin negru	81.2	40.3	9.0	gard E	14.5	gard S	4	F9-11	Dud alb	85.1	27.7	6.1	gard E	25.9	gard N
4	A34-4	Pin negru	77.6	46.8	7.9	gard S	12.0	gard E	4	S17-1	Oțetar	48.9	29.9	23.9	gard S	28.9	gard N
4	A34-5	Pin negru	74.6	46.7	7.9	gard S	15.1	gard E	4	S3-4	Iasomie falsă	54.5	41.8	12.2	gard S	35.4	gard E
4	A34-6	Pin negru	71.5	46.7	7.8	gard S	18.1	gard E	4	S6-6	Hibiscus	47.6	44.5	9.3	gard S	42.1	gard E
4	A34-7	Pin negru	68.5	46.6	7.8	gard S	21.1	gard E	4	S6-7	Hibiscus	47.6	41.9	12.0	gard S	40.9	gard N
4	A34-8	Pin negru	65.6	46.5	7.8	gard S	24.0	gard E	4	ar9-1	Roiniță	52.6	43.0	10.9	gard S	37.3	gard E
4	A34-9	Pin negru	62.5	46.5	7.8	gard S	27.1	gard E	4	ar9-2	Roiniță	52.3	42.5	11.5	gard S	37.6	gard E
4	A34-10	Pin negru	59.5	46.3	7.8	gard S	30.1	gard E	4	ar9-3	Roiniță	51.9	41.9	12.0	gard S	38.0	gard E
4	A34-11	Pin negru	56.5	46.4	7.7	gard S	33.1	gard E	4	ip102-1	Lofantus	56.5	34.7	19.4	gard S	33.5	gard N
4	A34-12	Pin negru	80.3	42.9	9.7	gard E	11.8	gard S	4	ip102-2	Lofantus	55.5	35.0	19.1	gard S	33.8	gard N
4	A34-13	Pin negru	82.4	29.9	8.6	gard E	24.9	gard S	4	ip102-3	Lofantus	55.8	34.0	20.1	gard S	32.8	gard N
4	A34-14	Pin negru	50.5	46.2	7.7	gard S	39.1	gard E	4	ip102-4	Lofantus	55.0	39.1	14.9	gard S	35.2	gard E
4	A34-15	Pin negru	53.5	46.3	7.7	gard S	36.0	gard E	4	ip102-5	Lofantus	54.6	38.2	15.9	gard S	35.6	gard E
4	F10-1	Cireș	70.2	35.8	18.7	gard S	20.2	gard E	4	ip19-1	Tătăneasă	57.6	28.0	26.1	gard S	26.8	gard N
4	F15-1	Piersic	64.5	33.5	20.8	gard S	26.1	gard E									
4	F17-1	Păr	62.3	42.1	12.1	gard S	27.7	gard E									
4	F21-1	Corn	87.3	31.0	3.7	gard E	23.9	gard S									
4	F21-5	Corn	86.0	43.0	4.0	gard E	11.9	gard S									
4	F21-6	Corn	86.6	36.9	3.8	gard E	18.0	gard S									
4	F21-7	Corn	85.1	48.9	4.4	gard E	5.9	gard S									
4	F21-9	Corn	80.2	50.8	4.0	gard S	9.1	gard E									
4	F21-10	Corn	74.2	50.6	4.0	gard S	15.1	gard E									
4	F21-11	Corn	68.2	50.5	3.9	gard S	21.1	gard E									
4	F21-12	Corn	62.2	50.3	4.0	gard S	27.1	gard E									
4	F21-13	Corn	56.2	50.2	3.9	gard S	33.1	gard E									